

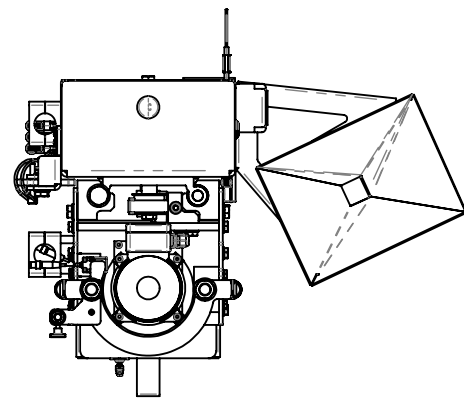
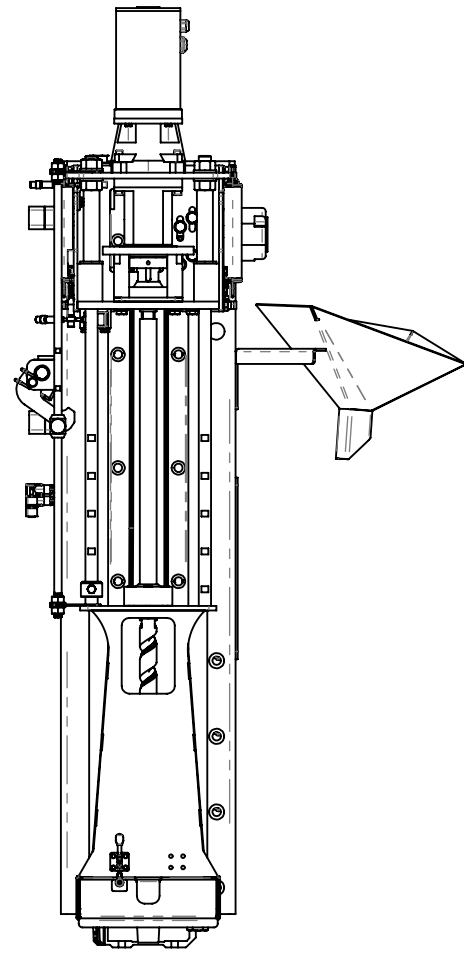
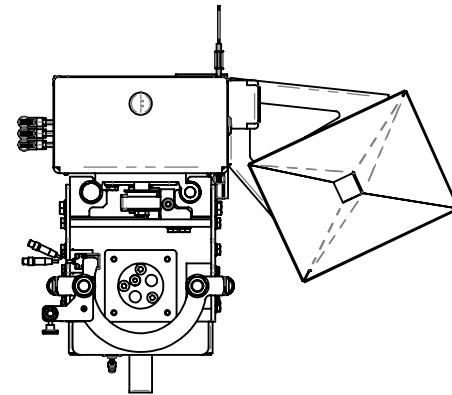
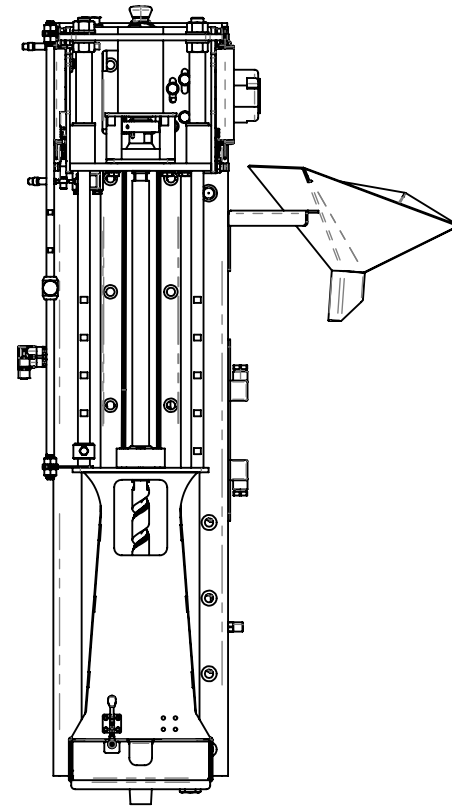


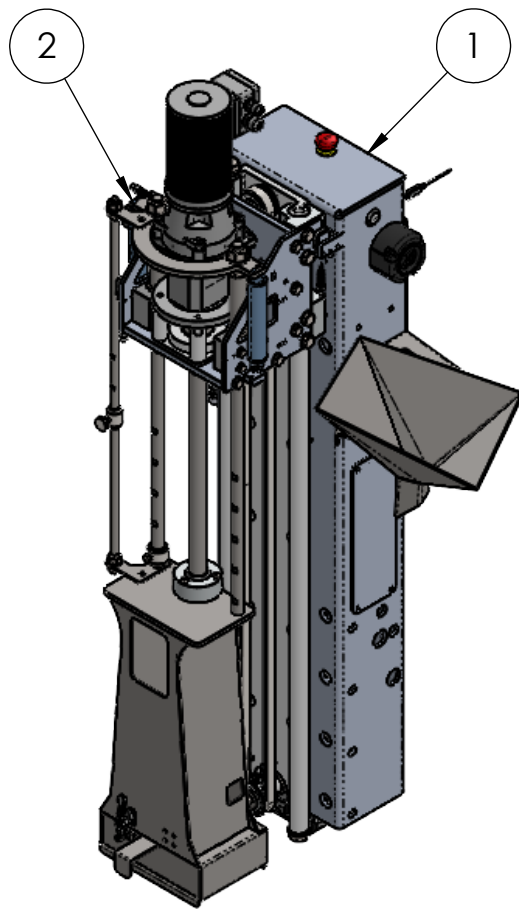


DE-1.30

Betriebsspannung: 24 VDC
Strombedarf max.: 50A

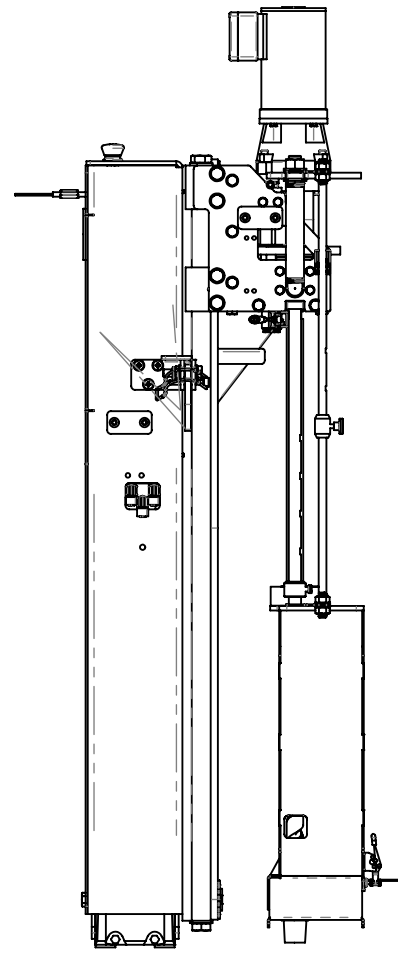

DH-1.30

Volumenstrom: 16 - 20 l/min
Arbeitsdruck: 100 bar
Steuerspannung: 12 VDC

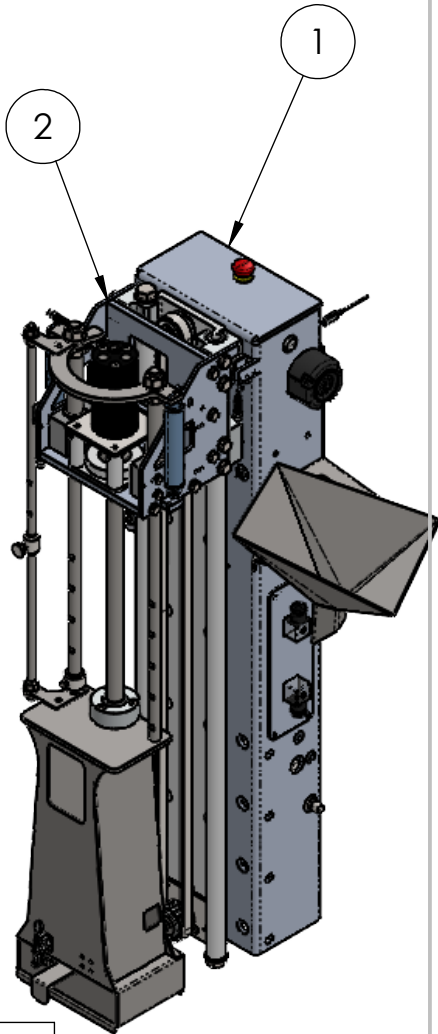


POS-NR.	Artikel-nummer	Benennung	MENGE
1	DH/DE.1	Turm	1
2	DH/DE.2	Schlitten	1

 BODENPROBETECHNIK PETERS		Allgemeintoleranzen DIN ISO 2768-m-S	Werkstückkanten DIN 6784	WERKSTOFF: Bodenprobetechnik Peters GmbH Am Fliegerhorst 11 D-49610 Quakenbrück	MABSTAB: 1:10 Tel.: 05431-936440 e-mail: info@bodenprobetechnik.de
NAME	DATUM	ÄNDERUNGSTEXT			
B.P.	27.09.2024	Erstfreigabe			
B.P	13.05.2026	Erdbehälter geändert, Ausschnitte im Turm ergänzt			
GEWICHT IN G: 47027					


DH/DE-1.30	
ZEICHNUNGSNR.	
Technische Daten	A3
Schutzvermerk ISO 16016 beachten	Blatt 2 v. 2
K:\DH_DE-1.30\	

POS-NR.	Artikel-nummer	Benennung	MENGE
1	DH.100.00-03	Aluprofil	1
2	DH.101.00	Linearführung	1
3	DH.102.00-01	Aludeckel unten	1
4	DH.103.00-02	Aludeckel oben	1
5	DE.104.00	Elektr. Hubantrieb	1
6	DH.104.00	Hydr. Hubantrieb	1
7	Z-DH.104.04	Zahnriemenscheibe	1
8	Z-DH.104.05	Umlenkrolle	1
9	Z-DH.104.06	Zahnriemen	1
10	DH.105.00-01	Distanzscheibe	1
11	DH.106.00	Transportsicherung	1
12	DH.107.00	Sensor Abstandsflach	1
13	DE.109.00	Schaltschrank	1
14	Z-DH.109.01	Gehäuse	1
15	DH.111.00-01	Trichter	1
16	DH.114.00	Deckel Ventileinheit	1
17	DH.115.00	Steckdosendeckel	1
18	DH.116.00	Ventileinheit vormontiert	1
19	N6.110.05-01	Transportsicherung fix	1
20	Z-N6.301.00	Sensor	1
21	Z-00005	KFZ Steckdose 13P 12V	1
22	Z-00073	Sechskanmutter mit Klemmteile	1
23	Z-00092	Unterlegscheibe	1
24	Z-00099	Sechskantschraube mit Schaft	1
25	Z-00189	Not-Halt-Taster mit Kontakten	1
26	Z-00154	Sensorkabel M12 Rohling	4
27	Z-00215	Drucktaster weiß	1
28	Z-00232	2/2 Wegeventil	1
29	Z-00233	Druckminderventil	1

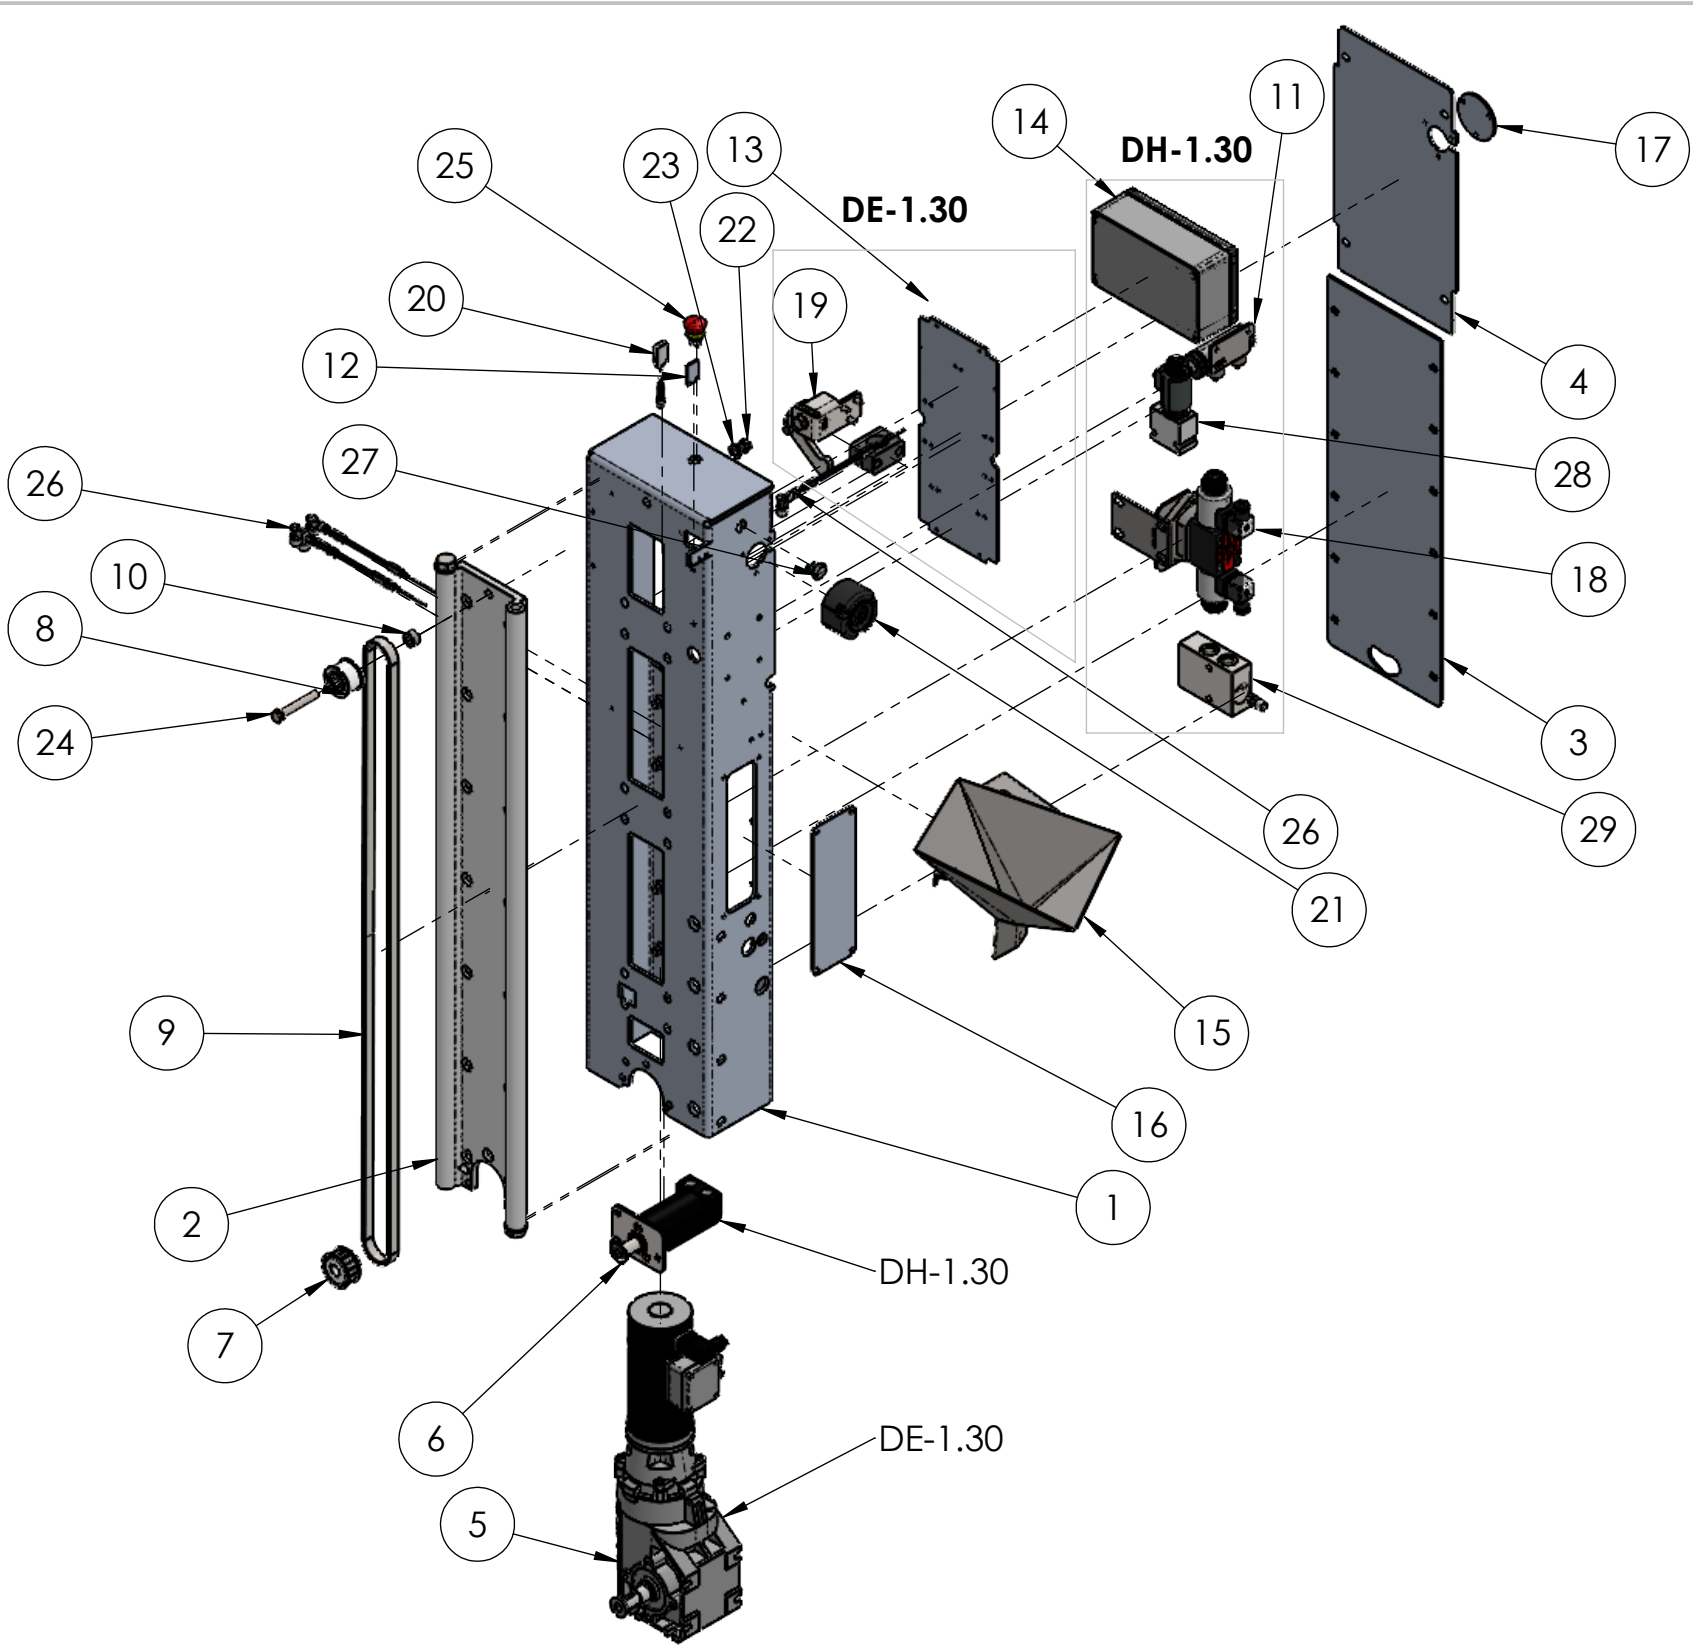

			Allgemeintoleranzen	Werkstückkanten	WERKSTOFF:	MABSTAB: 1:10
			DIN ISO 2768-m-S	DIN 6784	Bodenprobetechnik Peters GmbH Am Fliegerhorst 11 D-49610 Quakenbrück	Tel.: 05431-936440 e-mail: info@bodenprobetechnik.de
NAME	DATUM	ÄNDERUNGSTEXT	Turm			
B.P.	27.09.2024	Erstfreigabe				
			ZEICHNUNGSNR. DH/DE.1			
			Technische Daten			
			Schutzvermerk ISO 16016 beachten			
			A3			
GEWICHT IN G: 40188			Blatt 1 v. 2			
			K:\DH_DE-1.30\DH.1_Turm\			

Optional zweite Tiefe

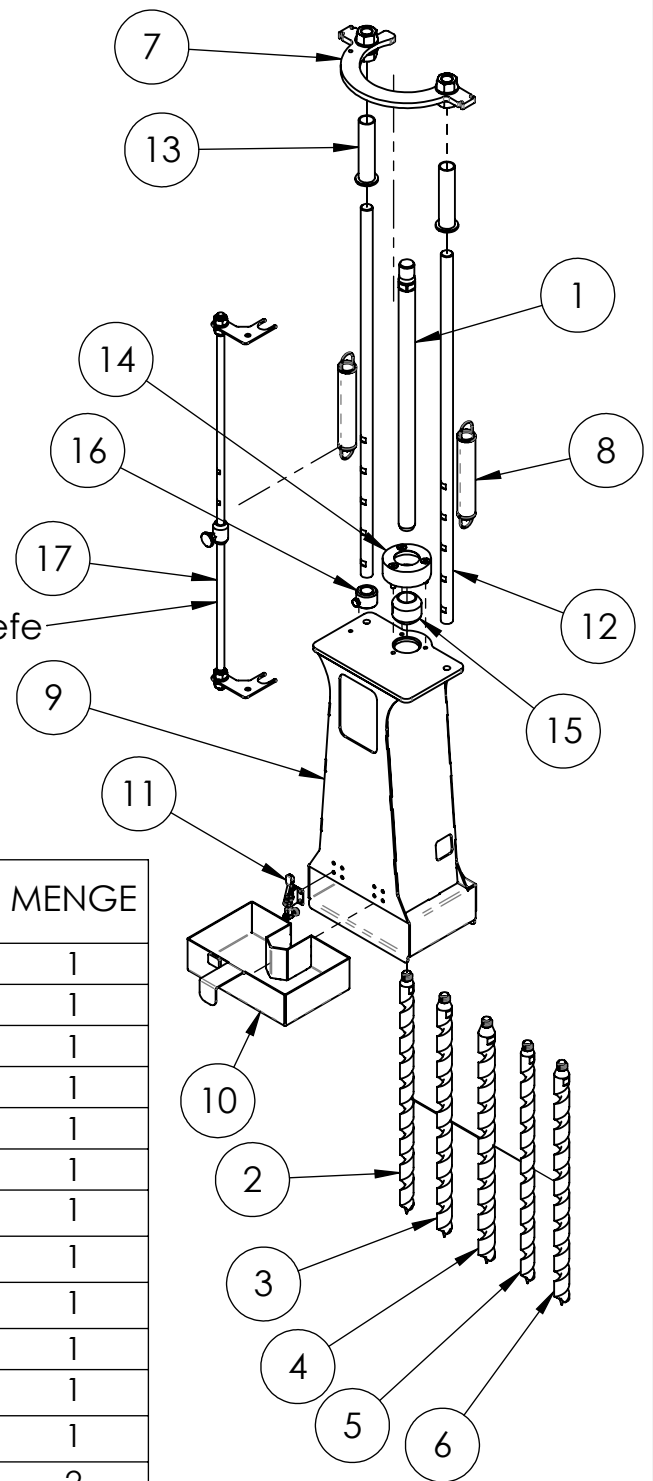

POS-NR.	Artikelnummer	Benennung	MENGE
1	DH.203.01-02	Welle	1
2	DH.203.04-01	Bohrer 18mm verschleißfest	1
3	DH.203.05-01	Bohrer 20mm verschleißfest	1
4	DH.203.06	Bohrer 22mm	1
5	DH.203.07	Bohrer 18mm	1
6	DH.203.08	Bohrer 20mm	1
7	DH.207.00-01	Federjoch	1
8	DH.215.00	Zugfedern	1
9	DH.216.01-03	Bodentopf	1
10	DH.216.09-02	Schubblade	1
11	Z-DH.216.13	Spannhebel	1
12	DH.217.00	Führungstangen	1
13	DH.218.00-01	Stützrohr	2
14	DH.220.01-01	Lagerschale	1
15	DH.220.02	Kunststoffeinsatz	1
16	DH.221.01	Tiefenbegrenzer	1
17	DH.223.00-01	Gestänge für zweite Tiefe	1



Allgemeintoleranzen
DIN ISO
2768-m-S

Werkstückkanten
DIN 6784

WERKSTOFF:

Bodenprobetechnik Peters GmbH
Am Fliegerhorst 11
D-49610 Quakenbrück

Tel.: 05431-936440
e-mail: info@bodenprobetechnik.de

MAßSTAB: 1:10

NAME	DATUM	ÄNDERUNGSTEXT
B.P.	07.05.2026	Erstfreigabe

Erdbehälter vormontiert

ZEICHNUNGSNR.

DH.224.00

Technische Daten

Schutzvermerk ISO 16016 beachten


A4

Blatt 1 v. 1

GEWICHT IN G: 13195

K:\DH_DE-1.30\DH.2_Schliffen\DH.224.00_Erdbehälter vormontiert\

POS-NR.	Artikel-nummer	Benennung	MENGE
1	DH.200.00-02	Schlitten	1
2	DH.202.00	Lagerflansch	1
3	DE.203.02	Zwischenzapfen Elektromotor	1
4	DH.203.02	Zwischenzapfen Hydromotor	1
5	DH.203.03	Spannring	1
6	DH.204.00	Motorplatte	1
7	DH.205.00	Erdbehälterführung	1
8	DH.206.01	Lagergehäuse	4
9	DH.208.00-01	Gewindewinkel	1
10	DH.209.00-01	Spannwinkel	1
11	Z-DE.210.00	Bohrmotor	1
12	DH.211.00	Klemmplatte	2
13	DH.213.00-01	Sensorhalter	1
14	DH.214.00	Distanzstück Motor	4
15	Z-N6.210.00	Hydraulikmotor 32	1
16	Z-N6.211.01	Gleitfolie	4
17	Z-N6.301.00	Sensor	3
18	Z-00084	Unterlegscheibe	1
19	Z-00236	Sicherungsring außen	1
20	Z-00237	Radialrillenkugellager Ø30mm	1
21	Z-00238	Zylinderschraube mit Innensechskant und Schaft	1

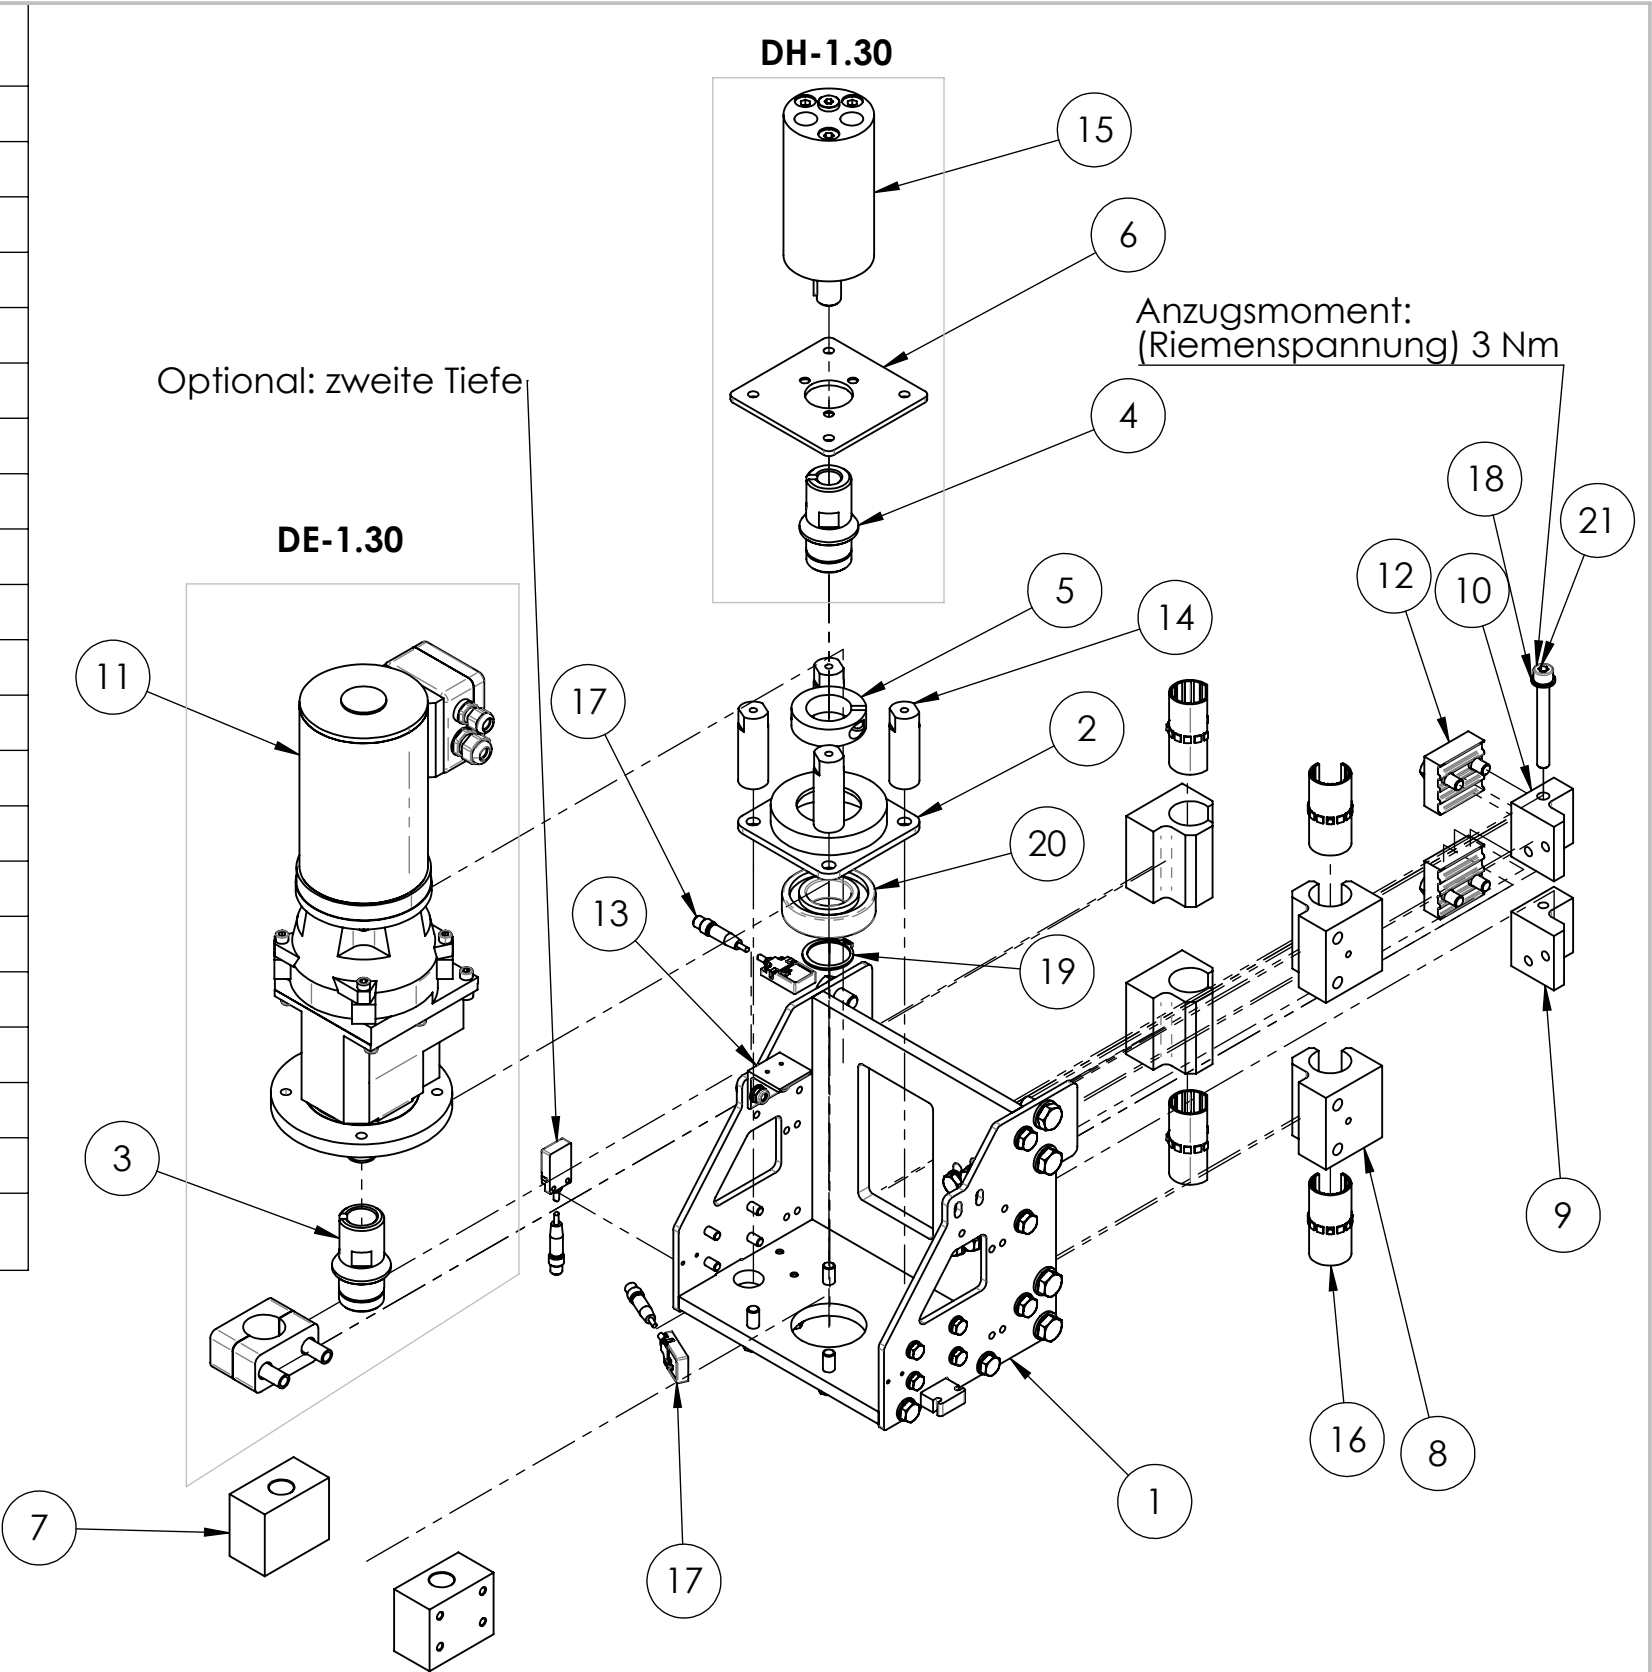

			Allgemeintoleranzen	Werkstückkanten	WERKSTOFF:	MABSTAB: 1:5
			DIN ISO 2768-m-S	DIN 6784	Bodenprobetechnik Peters GmbH Am Fliegerhorst 11 D-49610 Quakenbrück	Tel.: 05431-936440 e-mail: info@bodenprobetechnik.de
NAME	DATUM	ÄNDERUNGSTEXT	Schlitten vormontiert			
B.P.	08.05.2026	Erstfreigabe				
			ZEICHNUNGSNR. DH.225.00			
			Technische Daten			
			Schutzvermerk ISO 16016 beachten			
			A3			
			Blatt 1 v. 1			
GEWICHT IN G: 13490			K:\DH_DE-1.30\DH.2_Schlitten\DH.225.00_Schlitten vormontiert\			