


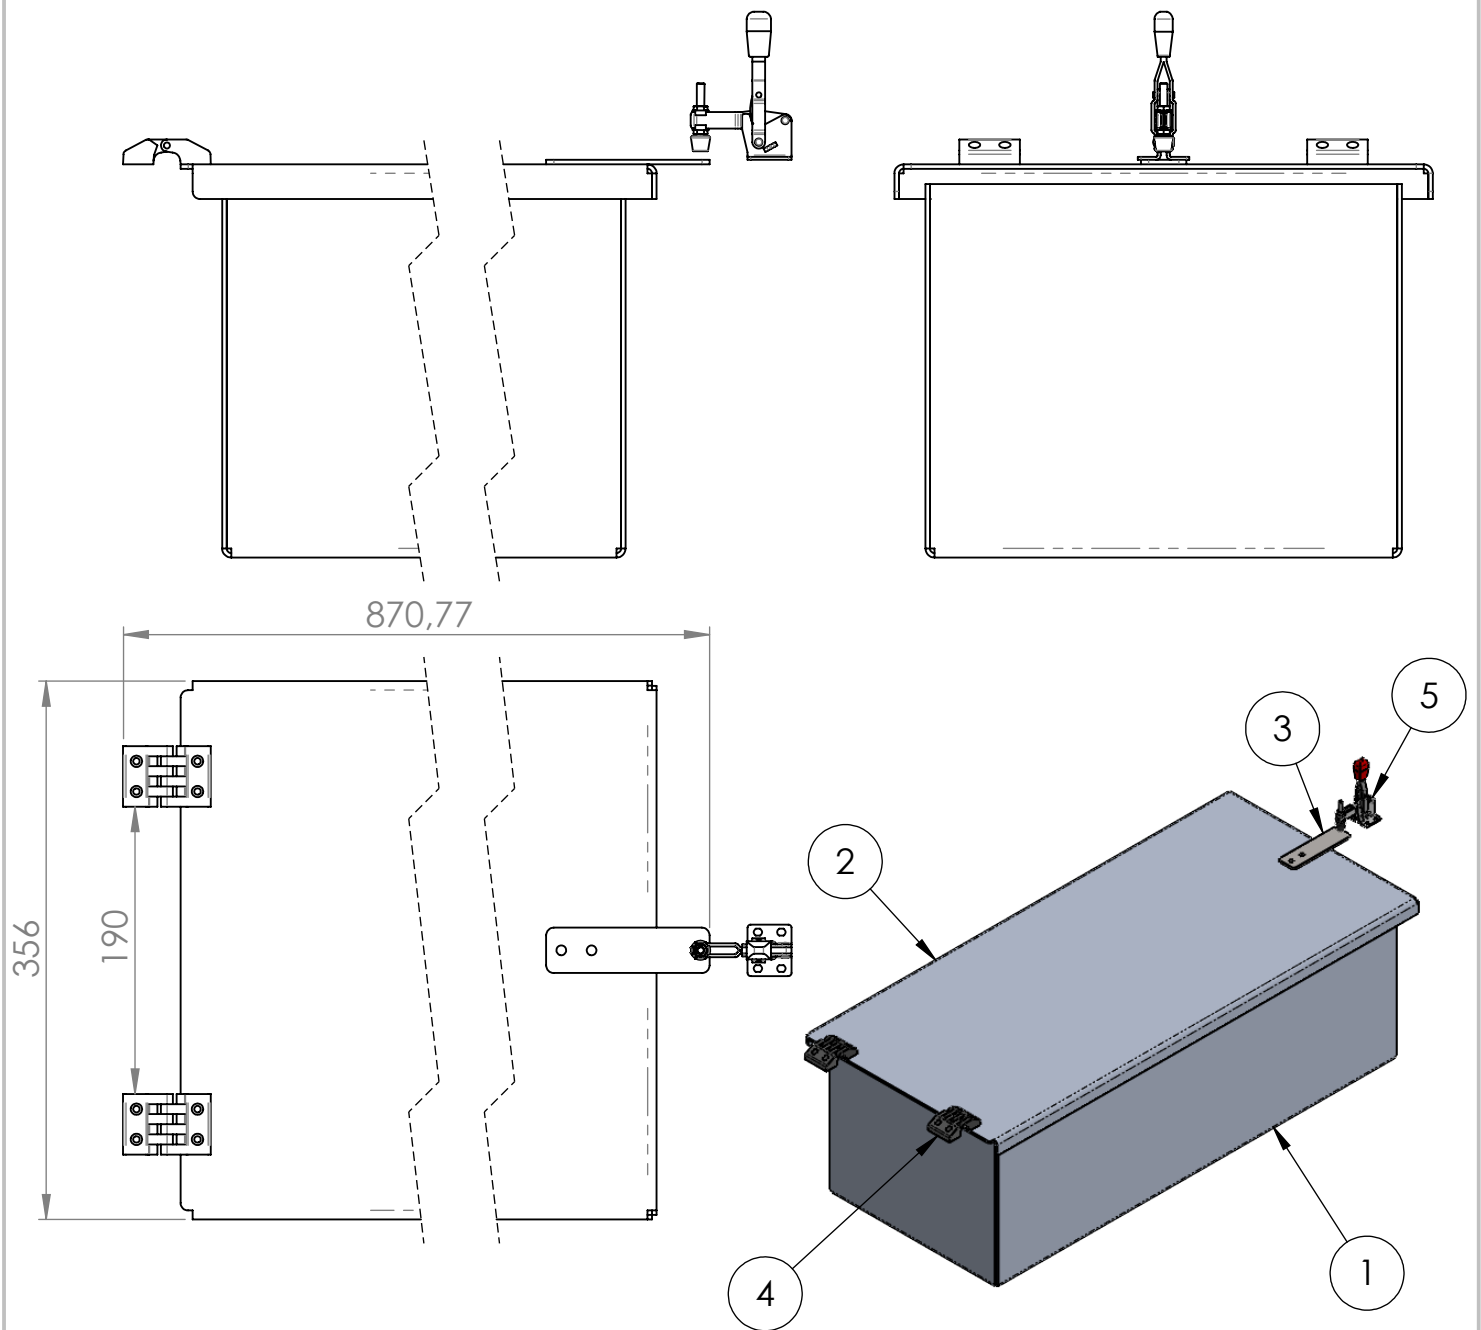

POS-NR.	Zeichnungsnummer	Benennung	MENGE	Technische Daten
1	B3.220.01	Staufachwanne	1	56L
2	B3.221.01	Staufachdeckel	1	
3	B3.221.02	Halteblech	1	
4	Z-B3.221.03	Scharnier Staufach	2	
5	Z-B3.221.04	Schnellspanner Staufach	1	

		Allgemeintoleranzen DIN ISO 2768-m-S	Werkstückkanten DIN 6784	WERKSTOFF: Bodenprobetechnik Peters GmbH Am Fliegerhorst 11 D-49610 Quakenbrück	MABSTAB: 1:5 Tel.: 05431-936440 e-mail: info@bodenprobetechnik.de
NAME B.P.	DATUM 15.06.2026	ÄNDERUNGSTEXT Erstfreigabe	Wasserdichtes Staufach ZEICHNUNGSNR. B3.221.00 Technische Daten Schutzvermerk ISO 16016 beachten		
GEWICHT IN G: 8708			K:\Boprob III\B3_2.Verkleidung\B3.221.00_Wasserdichtes Staufach\		