






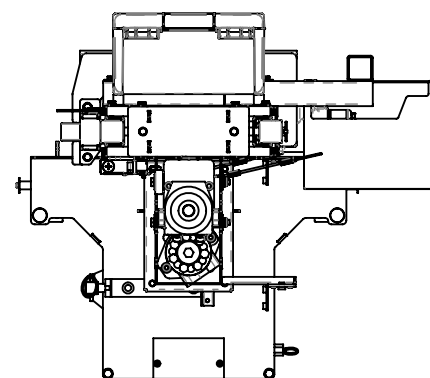



Abb. ähnlich.

 BODENPROBETECHNIK PETERS			Allgemeintoleranzen DIN ISO 2768-m-S	Werkstückkanten DIN 6784	WERKSTOFF: Bodenprobetechnik Peters GmbH Am Fliegerhorst 11 D-49610 Quakenbrück		MAßSTAB: 1:15 Tel.: 05431-936440 e-mail: info@bodenprobetechnik.de	
NAME	DATUM	ÄNDERUNGSTEXT			Multiprob			
B.P.	27.03.2024	Erstfreigabe						
					ZEICHNUNGSNR.			
					Technische Daten Schutzvermerk ISO 16016 beachten			
GEWICHT IN G: 228508,70					A3 Blatt 2 v. 2			
C:\Users\User\OneDrive - Bodenprobetechnik Peters GmbH\Fertigung\Zeichnungen\MP-1_2_3_4\								

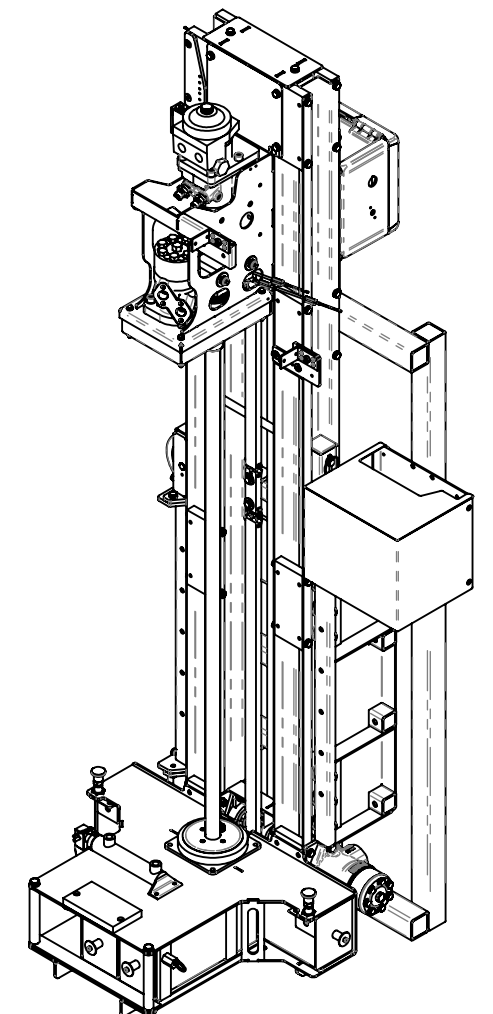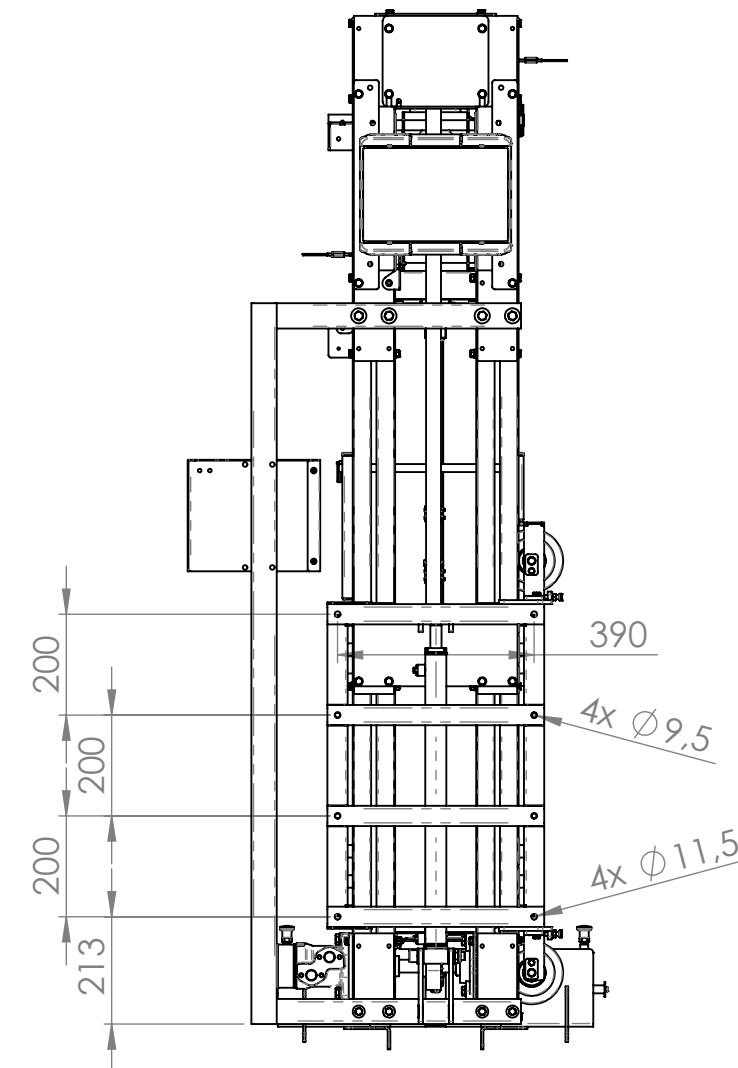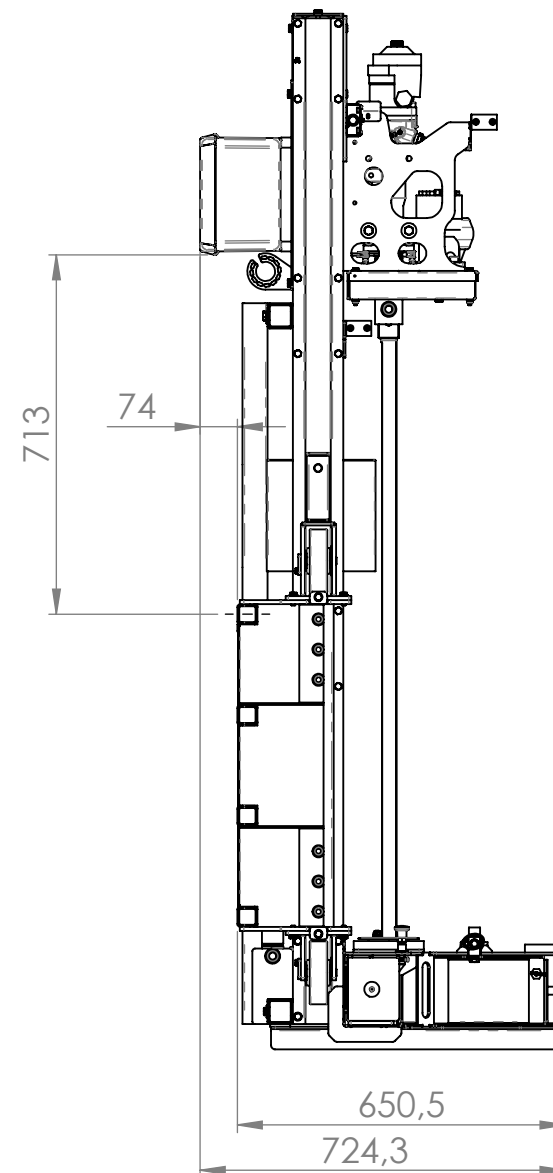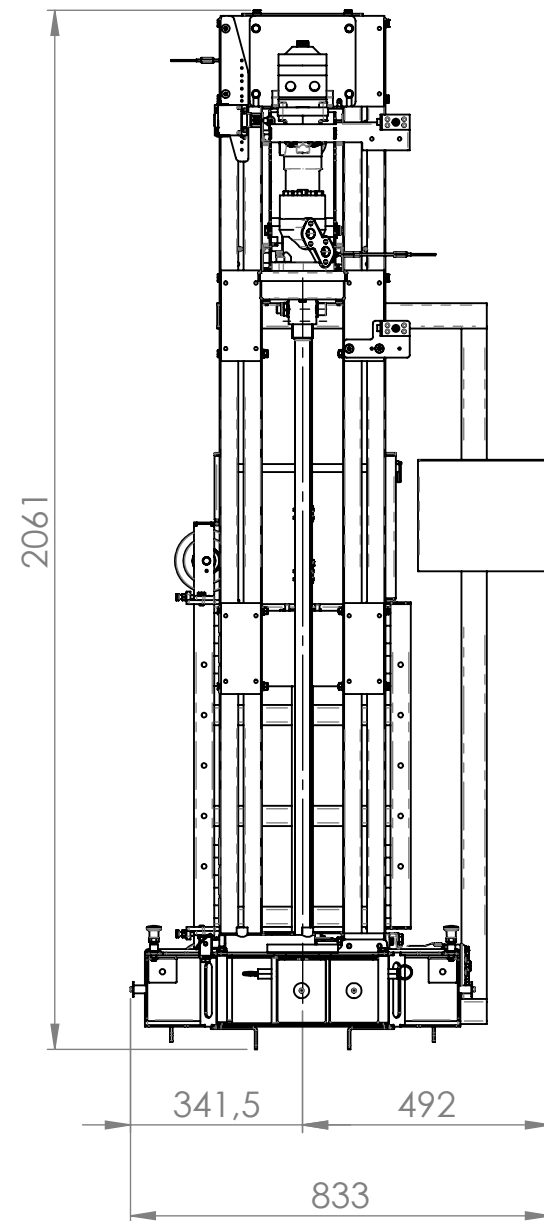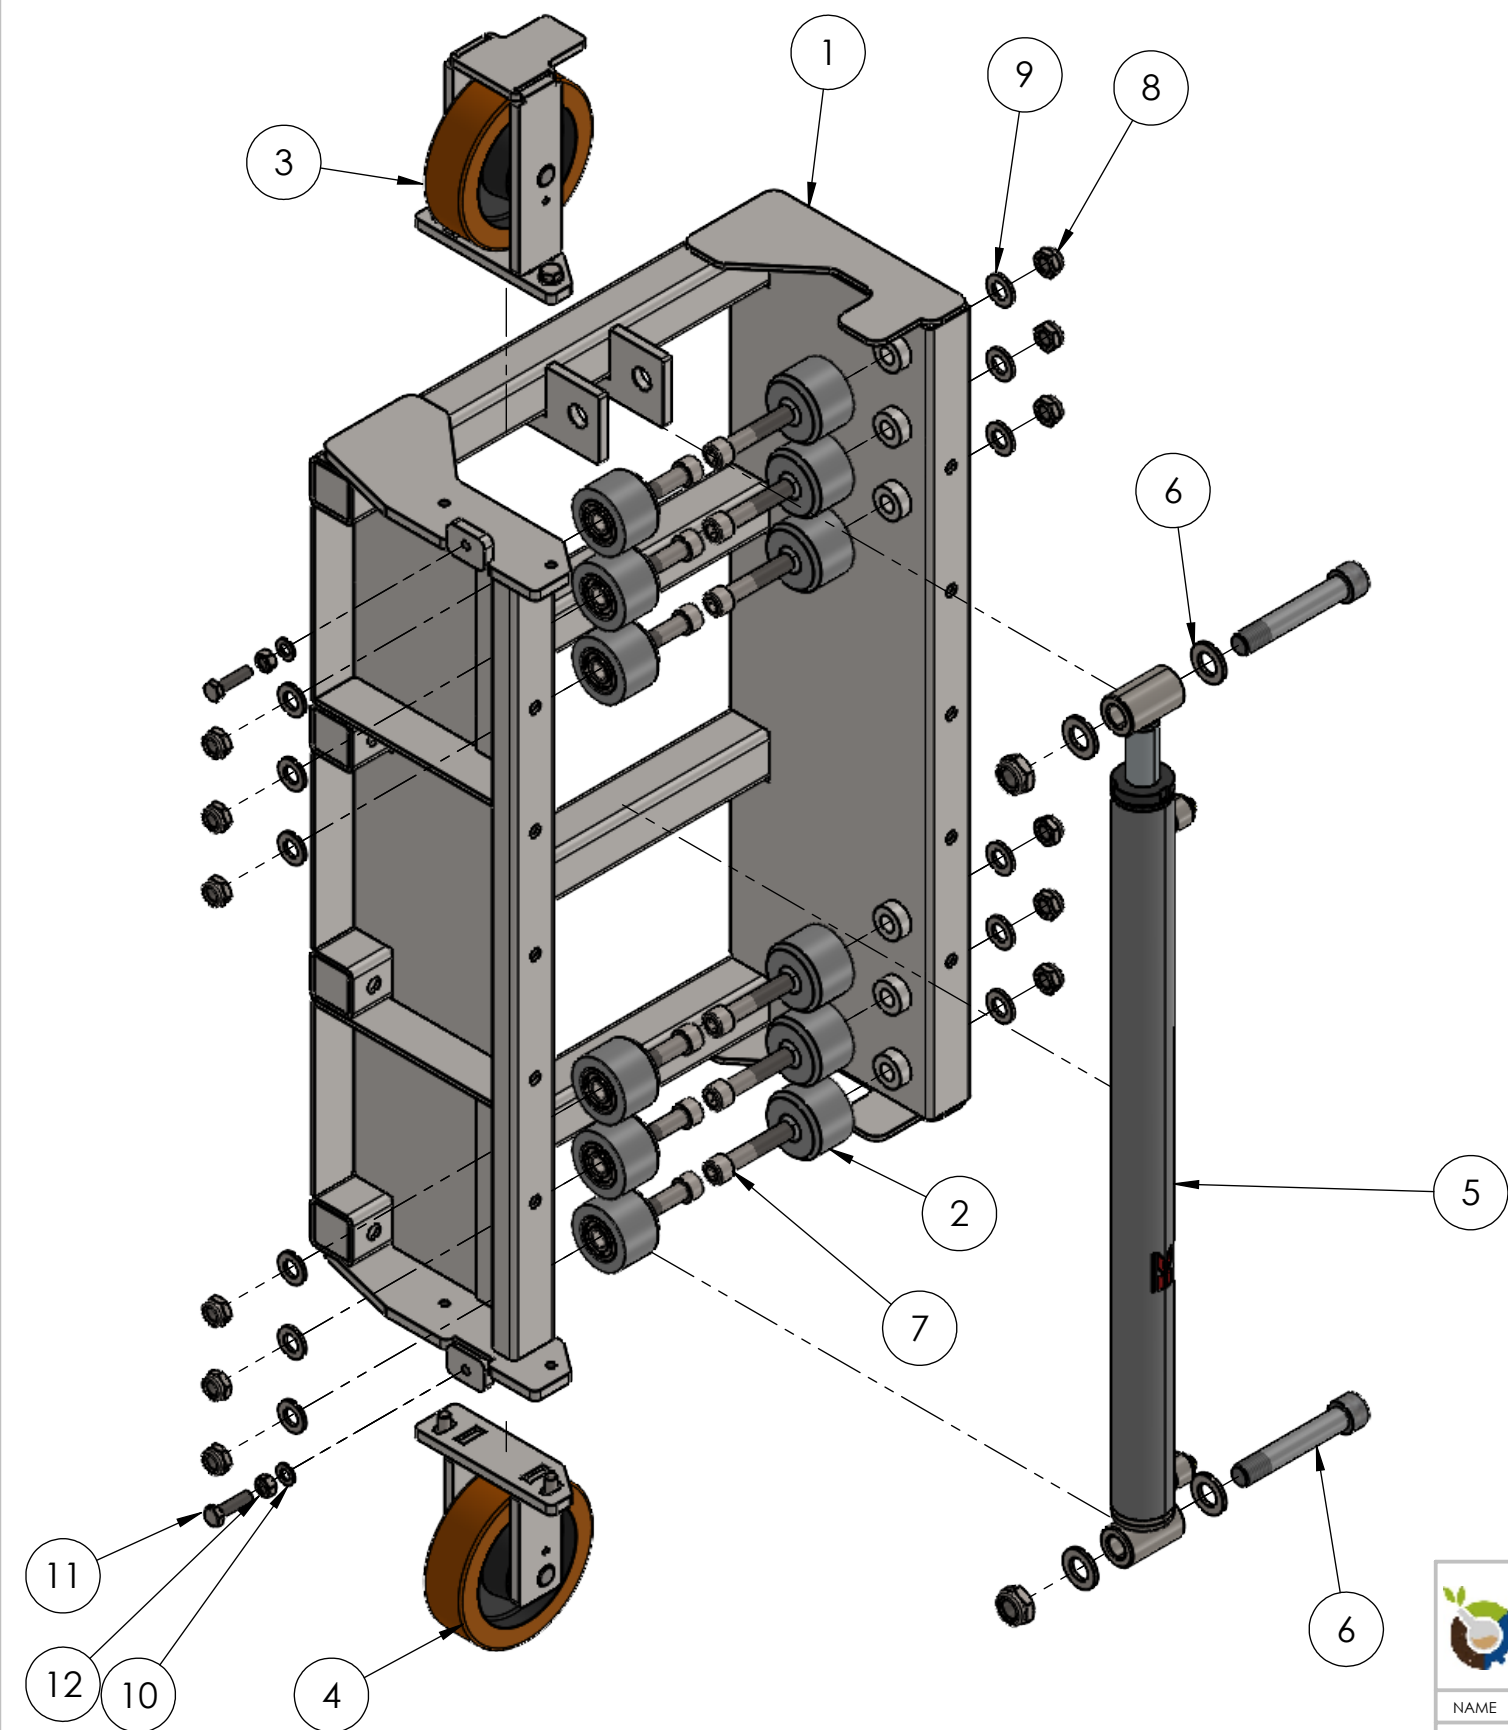


POS-NR.	Artikel-nummer	Benennung	MENGE
1	UP.100.00-01	Tragegestell SBG	1
2	UP.101.00-01	Laufrolle komplett	12
3	MP.103.00	Seitl. Führungsrolle oben	1
4	MP.104.00	Seitl. Führungsrolle unten	1
5	Z-UP.105.00	Hydraulikzylinder	1
6	UP.106.00	Verbindungsbolzen Hydraulikzylinder	2
7	Z-00059	Zylinderschraube mit Innensechskant und Schaft	12
8	Z-00080	Sechskantmutter mit Klemmteile	12
9	Z-00081	Unterlegscheibe	12
10	Z-00084	Unterlegscheibe	2
11	Z-00085	Sechskantschraube	2
12	Z-00088	Sechskantmutter	2



			Allgemeintoleranzen	Werkstückkanten	WERKSTOFF:	MABSTAB: 1:5
			DIN ISO 2768-m-S	DIN 6784	Bodenprobetechnik Peters GmbH Am Fliegerhorst 11 D-49610 Quakenbrück	Tel.: 05431-936440 e-mail: info@bodenprobetechnik.de
NAME	DATUM	ÄNDERUNGSTEXT	Tragegestell			
B.P.	05.05.2024	Freigabe				
			ZEICHNUNGSNR. MP.1			
			Technische Daten			
			Schutzvermerk ISO 16016 beachten			
			A3			
GEWICHT IN G: 32669.80			Blatt 1 v. 3			

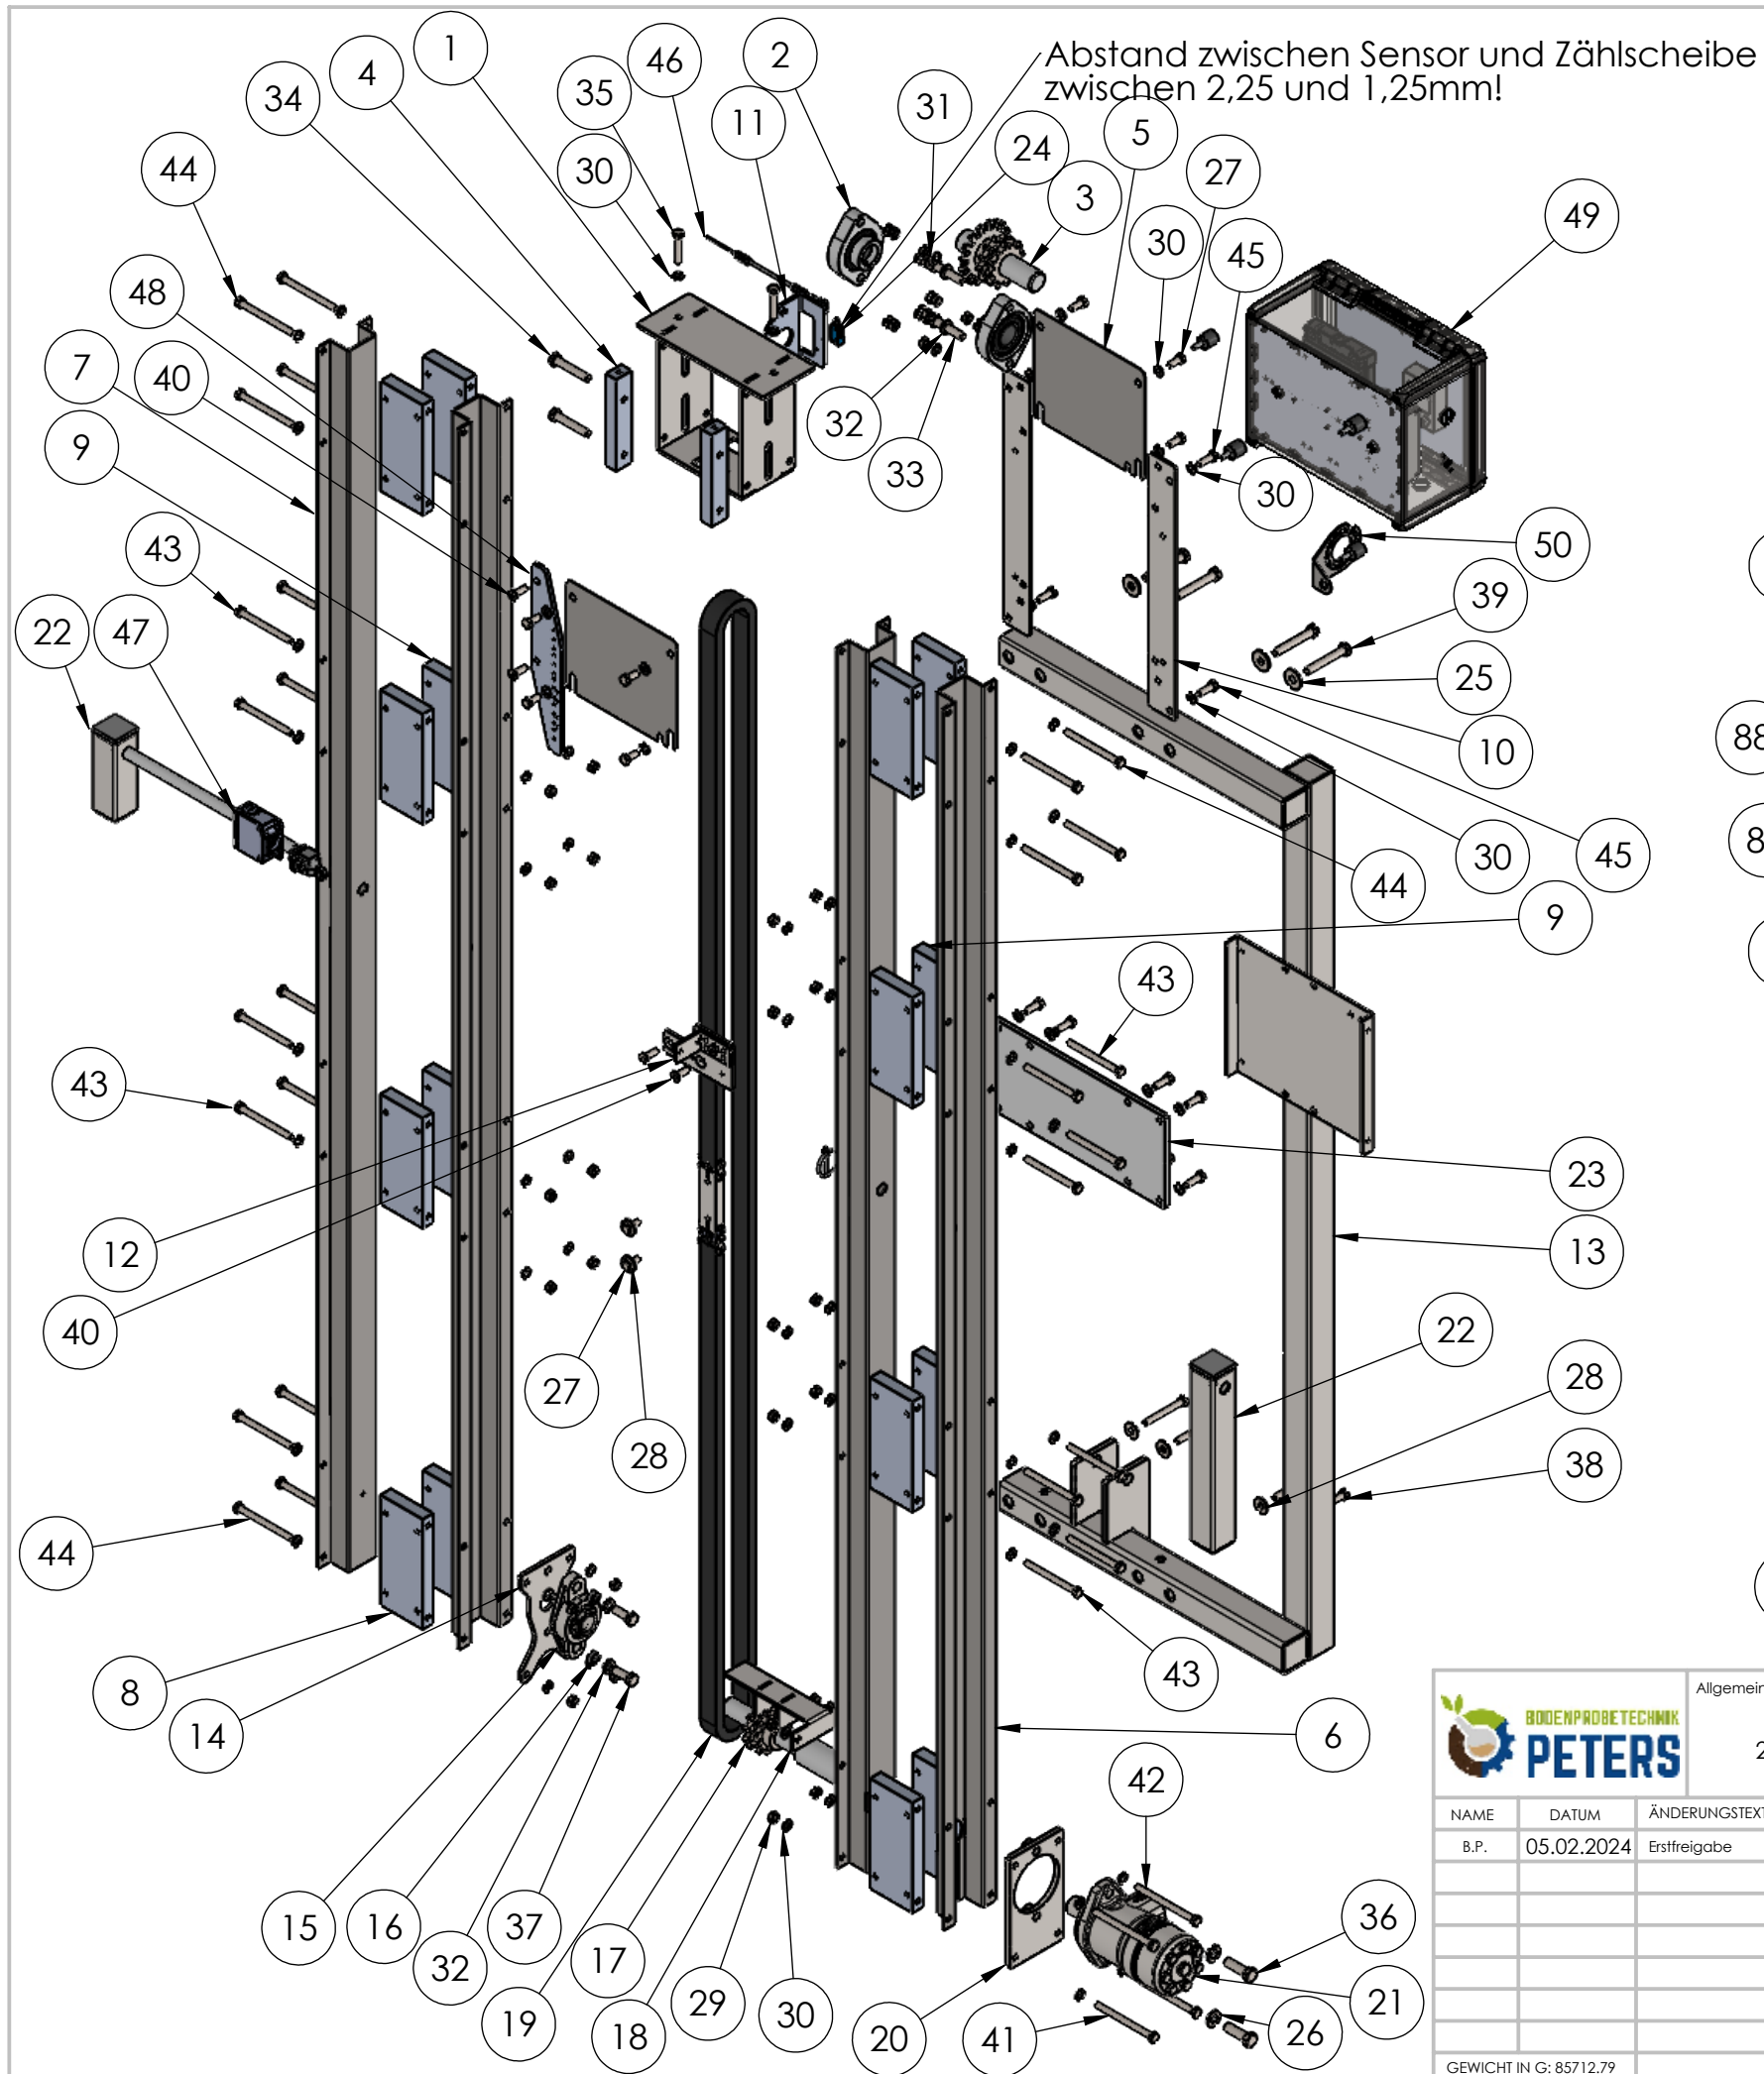

POS-NR.	Artikel-nummer	Benennung	MENGE
85	UP.218.02	Kettenanschlußverbinder	1
86	Z-UP.218.03	Rollenkette	1
87	Z-UP.218.04	Kettenschloss	2
88	Z-UP.218.05	Gekröpftes Kettenglied	1

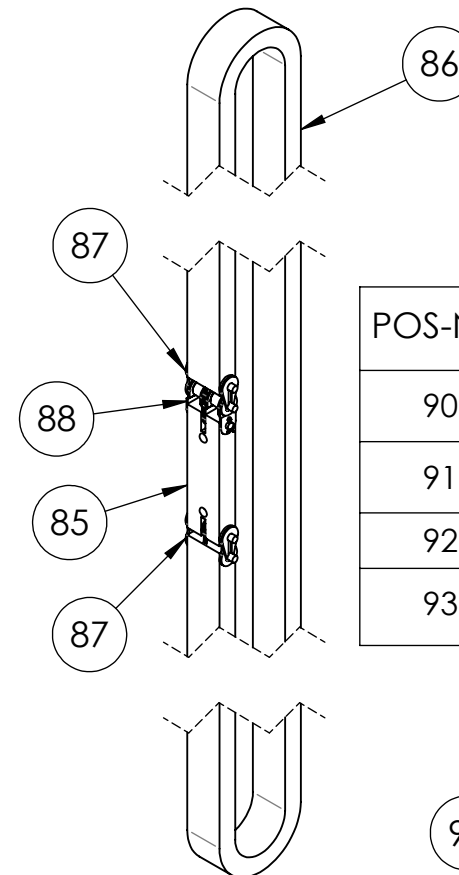

POS-NR.	Artikel-nummer	Benennung	MENGE
90	Z-UP.222.05	Deckel Vierkant	2
91	UP.222.06	Rohr mit Achse	1
92	UP.222.07	Rohr lose	1
93	Z-UP.223.00	Klappsplint	1

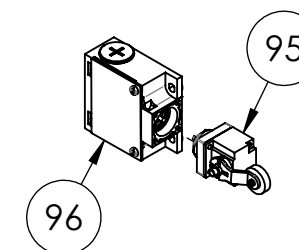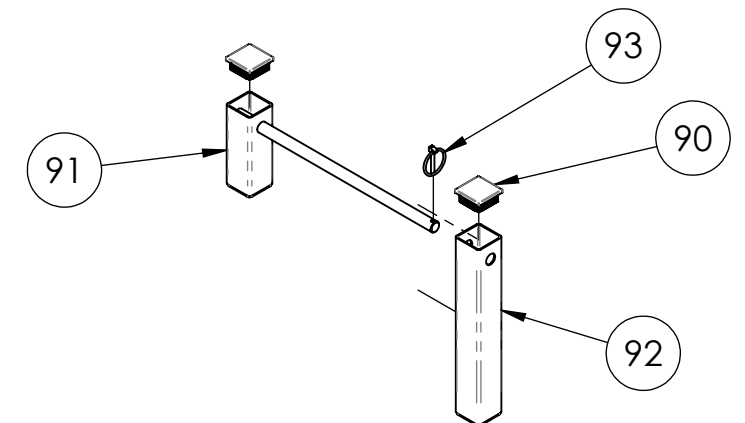


POS-NR.	Artikel-nummer	Benennung	MENGE
95	Z-00040	Endschalter	1
96	Z-00041	Endschaltergehäuse	1

			Allgemeintoleranzen DIN ISO 2768-m-S	Werkstückkanten DIN 6784	WERKSTOFF: Bodenprobetechnik Peters GmbH Am Fliegerhorst 11 D-49610 Quakenbrück	MABSTAB: 1:10
NAME B.P.	DATUM 05.02.2024	ÄNDERUNGSTEXT Erstfreigabe	Turm			
			ZEICHNUNGSNR. MP.2			
			Technische Daten Schutzvermerk ISO 16016 beachten			A3 Blatt 1 v. 3
GEWICHT IN G: 85712.79			C:\Users\User\OneDrive - Bodenprobetechnik Peters GmbH\Fertigung\Zeichnungen\MP-1_2_3_4\MP.2_Turm\			

POS-NR.	Artikel-nummer	Benennung	MENGE	POS-NR.	Artikel-nummer	Benennung	MENGE
1	UP.201.00-02	Kopfgehäuse	1	34	Z-00094	Sechskantschraube	2
2	Z-UP.202.00	Flanschlager Ø30mm	2	35	Z-00095	Sechskantschraube	2
3	MP-UP.203.00-02	Kettenradwelle oben	1	36	Z-00096	Sechskantschraube	2
4	UP.204.00	Spannklotz	2	37	Z-00097	Sechskantschraube	2
5	UP.205.00	Kopfgehäusedeckel	2	38	Z-00098	Sechskantschraube mit Schaff	4
6	UP.206.01-03	Profilschiene rechts	2	39	Z-00099	Sechskantschraube mit Schaff	4
7	UP.206.02-02	Profilschiene links	2	40	Z-00100	Senkschraube	4
8	UP.207.00-01	Alu-Distanzplatte	14	41	Z-00101	Sechskantschraube mit Schaff	2
9	UP.208.00-01	Alu-Distanzplatte M10	2	42	Z-00102	Sechskantschraube mit Schaff	2
10	UP.209.00-01	Schaltschrankhalterung	2	43	Z-00103	Sechskantschraube mit Schaff	16
11	MP-UP.210.00-02	Alu-Sensorhalterung	1	44	Z-00104	Sechskantschraube mit Schaff	12
12	MP.211.00	Energiekettenhalter	1	45	Z-00105	Sechskantschraube	12
13	MP.212.00	Ventilhaltebügel	1	46	Z-00111	Sensorkabel	1
14	UP.213.00-02	Anbauplatte Flanschlager unten	1	47	Z-00112	Endschalter	1
15	Z-UP.214.01	Flanschlager Ø25mm	1	48	UP.224.00	Endschalterhalterung	1
16	UP.214.02	Zentrierbuchse	2	49	UP.600.00	Schaltschrank	1
17	UP.215.00	Kettenradwelle unten	1	50	SDH.100.01	Steckdosenhalter	1
18	MP.216.00	Eingriffsicherung Kettenrad unten	1				
19	UP.218.00	Kette komplett	1				
20	UP.220.00-01	Anbauplatte für Hydromotor	1				
21	Z-UP.221.00	Hydraulikmotor 250	1				
22	UP.222.00	Absturzsicherung	1				
23	UP.225.00	Alu-Versteifungsplatte	1				
24	Z-00045	Sensor	1				
25	Z-00072	Unterlegscheibe	4				
26	Z-00081	Unterlegscheibe	2				
27	Z-00082	Sechskantschraube	10				
28	Z-00083	breite Unterlegscheibe	6				
29	Z-00088	Sechskantmutter	32				
30	Z-00084	Unterlegscheibe	86				
31	Z-00090	Sechskantmutter	2				
32	Z-00092	Unterlegscheibe	6				
33	Z-00093	Sechskantschraube mit Schaff	2				


			Allgemeintoleranzen DIN ISO 2768-m-S		Werkstückkanten DIN 6784		WERKSTOFF: Bodenprobetechnik Peters GmbH Am Fliegerhorst 11 D-49610 Quakenbrück		MAßSTAB: 1:13 Tel.: 05431-936440 e-mail: info@bodenprobetechnik.de		
NAME	DATUM	ÄNDERUNGSTEXT				Turm					
B.P.	05.02.2024	Erstfreigabe									
						ZEICHNUNGSNR. MP.2					
						Technische Daten					
						Schutzvermerk ISO 16016 beachten					
GEWICHT IN G: 85712.79			C:\Users\User\OneDrive - Bodenprobetechnik Peters GmbH\Fertigung\Zeichnungen\MP-1_2_3_4\MP.2_Turm\								

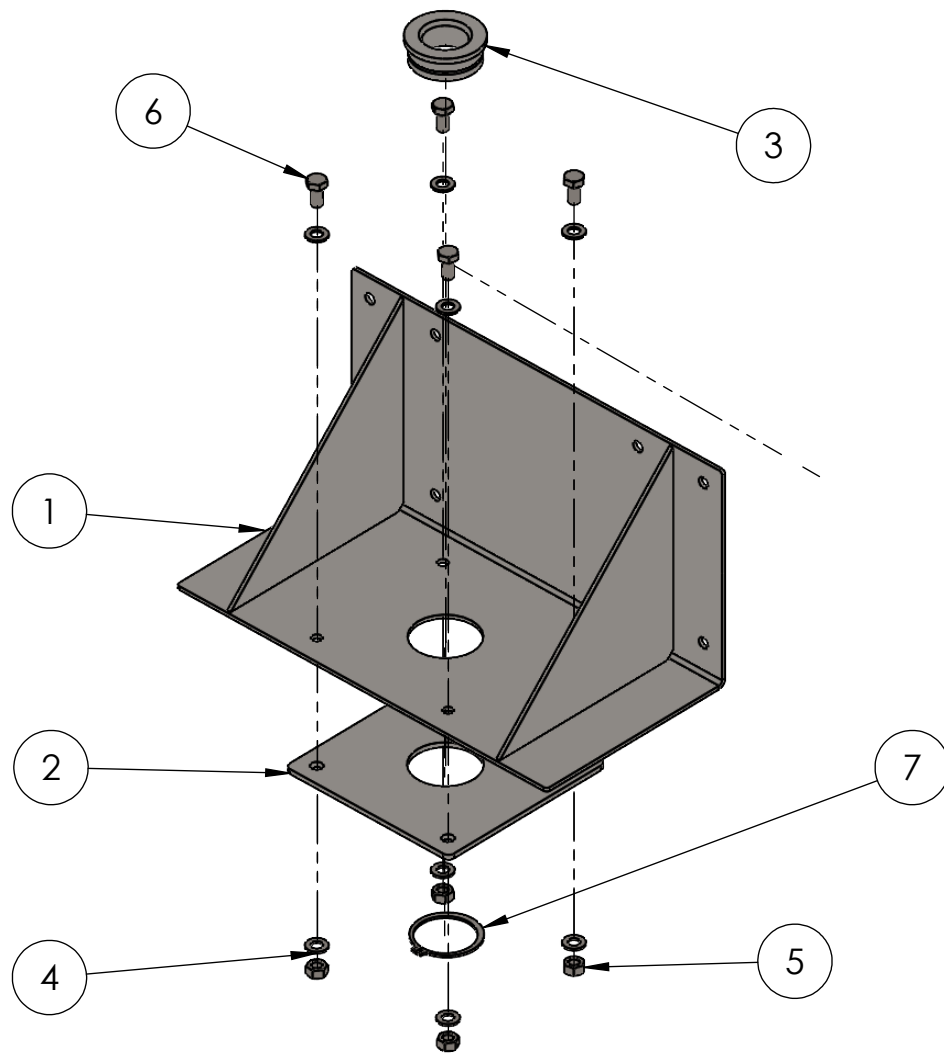

POS-NR.	Artikel-nummer	Benennung	MENGE
1	NH-UP.300.00	Fußplatte	1
2	NH-UP.303.00	Führungsplatte unten Bohrstock	1
3	NH-UP.304.00	Führungsbuchse d=31mm	1
4	Z-00084	Unterlegscheibe	8
5	Z-00088	Sechskantmutter	4
6	Z-00113	Sechskantschraube	4
7	Z-00155	Sicherungsring	1

 BODENPROBETECHNIK PETERS		Allgemeintoleranzen	Werkstückkanten	WERKSTOFF:	MABSTAB: 1:10	
		DIN ISO 2768-m-S	DIN 6784	Bodenprobetechnik Peters GmbH Am Fliegerhorst 11 D-49610 Quakenbrück	Tel.: 05431-936440 e-mail: info@bodenprobetechnik.de	
NAME	DATUM	ÄNDERUNGSTEXT			Fußplatte	
B.P.	25.03.2024	Erstfreigabe				
					ZEICHNUNGSNR. MP1.3	
					Technische Daten Schutzvermerk ISO 16016 beachten	A4
GEWICHT IN G: 4125.92		C:\Users\User\OneDrive - Bodenprobetechnik Peters GmbH\Fertigung\Zeichnungen\MP-1_2_3_4\MP.3_Magazin_Fuß\				


POS-NR.	Artikelnummer	Benennung	MENGE
1	MP-UP.3000.00-02	Magazingehäuse	1
2	MP-UP.3001.00-01	Erdbehälter links	1
3	MP-UP.3002.00-01	Erdbehälter rechts	1
4	MP-UP.3003.00-01	Erdbehälter mitte	1
5	Z-MP-UP.304.01	Rastbolzen mit Rastsperre	3
6	MP-UP.3005.00	Verschleißplatte	1
7	DP-UP.309.00	Griff	3
8	MP.310.00	Lagerflansch	1
9	DP-UP.312.00	Ausräumnabe 15mm	1
10	MP-UP.314.00-01	Ausräumer 15mm	1
11	DP-UP.317.00-02	Abdeckblech Nabe	1
12	MP-UP.3022.00-01	Magazinverstärkungswinkel rechts	1
13	MP-UP.3023.00-01	Magazinverstärkungswinkel links	1
14	Z-00066	Sicherungsring außen	3
15	Z-00067	Radialrillenkugellager	1
16	Z-00072	Unterlegscheibe	2
17	Z-00073	Sechskantmutter mit Klemmteile	4
18	Z-00082	Sechskantschraube	4
19	Z-00084	Unterlegscheibe	11
20	Z-00092	Unterlegscheibe	6
21	Z-00099	Sechskantschraube mit Schaft	2
22	Z-00113	Sechskantschraube	4
23	Z-00114	Sechskantschraube	2
24	Z-00115	Sechskantschraube	3
25	Z-00116	Senkschraube	2
Alternativer Ausräumer und zugehörige Ausräumnabe. Bohrstock beachten!			
27	MP-UP.315.00-01	Ausräumer 12mm	1
28	DP-UP.312.00	Ausräumnabe 12mm	1

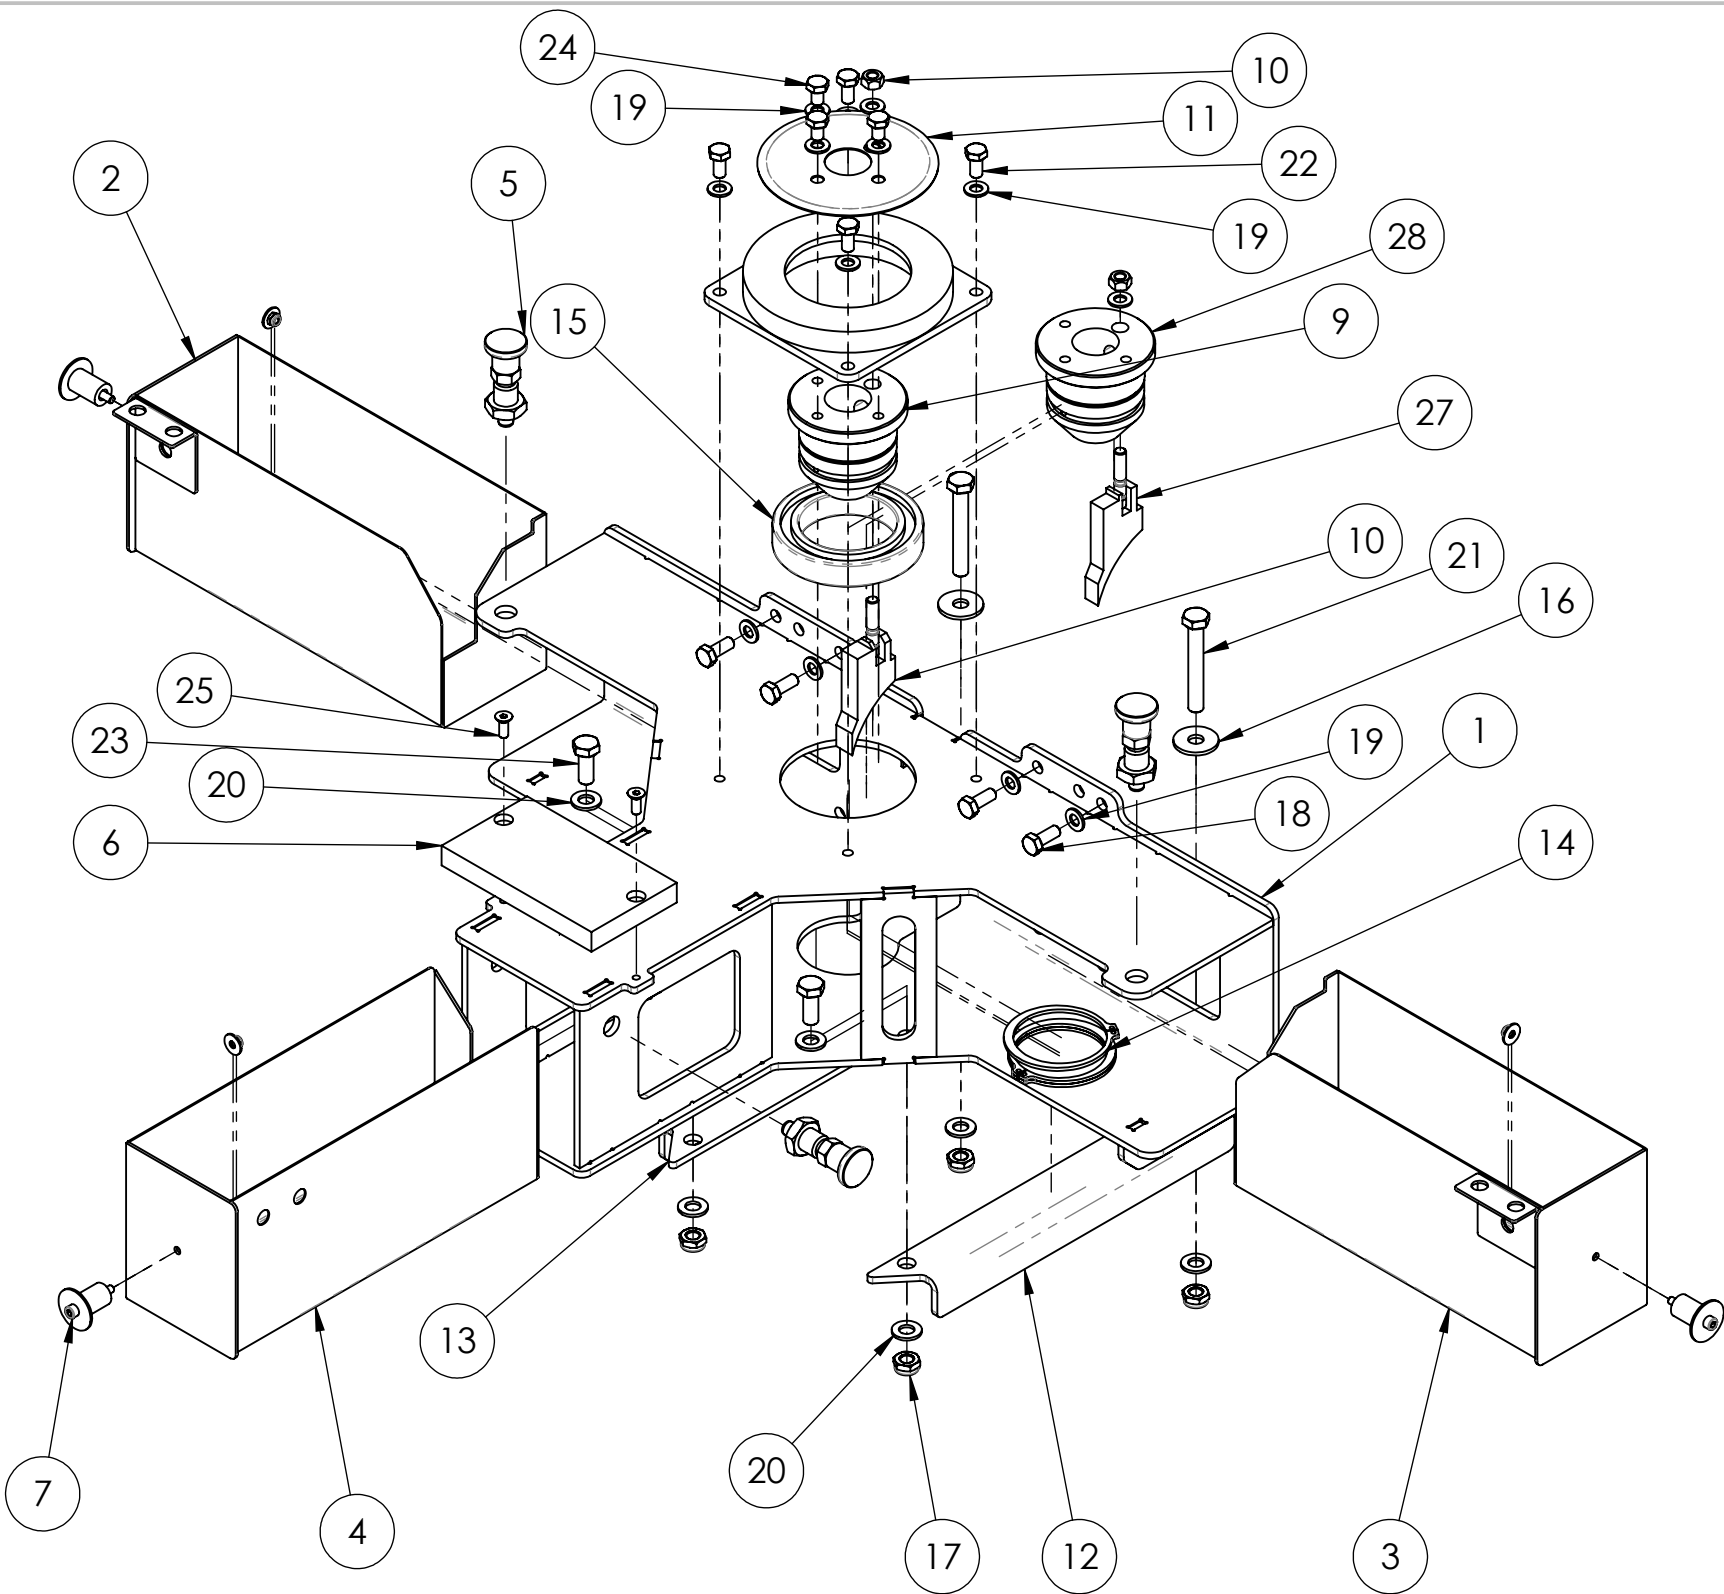

Sägelänge in mm:


			Allgemeintoleranzen	Werkstückkanten	WERKSTOFF:	MABSTAB: 1:5
			DIN ISO 2768-m-S	DIN 6784	Bodenprobetechnik Peters GmbH Am Fliegerhorst 11 D-49610 Quakenbrück	Tel.: 05431-936440 e-mail: info@bodenprobetechnik.de
NAME	DATUM	ÄNDERUNGSTEXT	Sternmagazin			
B.P.	07.02.2024	Erstfreigabe				
			ZEICHNUNGSNR. MP3.3			
			Technische Daten			
			Schutzvermerk ISO 16016 beachten			
			A3			
			Blatt 1 v. 2			
GEWICHT IN G: 22099			C:\Users\User\OneDrive - Bodenprobetechnik Peters GmbH\Fertigung\Zeichnungen\MP-1_2_3_4\MP.3_Magazin_FuB\			

POS-NR.	Artikel-nummer	Benennung	MENGE
1	MP4.300.00	Magazingehäuse	1
2	DP-UP.302.00-01	Eckpfosten	2
3	DP-UP.303.00	Verschiebeschlitten	1
4	Z-DP-UP.304.00	Rastbolzen	2
5	Z-MP-UP.304.01	Rastbolzen mit Rastsperre	2
6	Z-DP-UP.305.00	Klappsplint 6mm	1
7	DP-UP.306.00	Einstellschiene	1
8	DP-UP.307.00	Schublade links	1
9	DP-UP.308.00	Schublade rechts	1
10	DP-UP.309.00	Griff	4
11	MP.310.00	Lagerflansch	1
12	DP-UP.312.00	Ausräumnabe 15mm	1
13	MP-UP.314.00-01	Ausräumer 15mm	1
14	DP-UP.317.00-02	Abdeckblech Nabe	1
15	MP4.321.00	Magazinverstärkungswinkel links	1
16	MP4.322.00	Magazinverstärkungswinkel rechts	1
17	DP-UP.323.00	Verschiebezylinder	1
18	MP4.330.01	Distanzplatte	2
19	MP4.331.00	Distanzscheibe Verstärkungswinkel	2
20	MP-UP.3001.00-01	Erdbehälter links	1
21	MP-UP.3002.00-01	Erdbehälter rechts	1
22	MP-UP.3005.00	Verschleißplatte	1
23	Z-00067	Radialrillenkugellager	1
24	Z-00066	Sicherungsring außen	3
25	Z-00092	Unterlegscheibe	2
26	Z-00114	Sechskantschraube	2
Alternativer Ausräumer und zugehörige Ausräumnabe. Bohrstock beachten!			
28	MP-UP.315.00-01	Ausräumer 12mm	1
29	DP-UP.312.00	Ausräumnabe 12mm	1

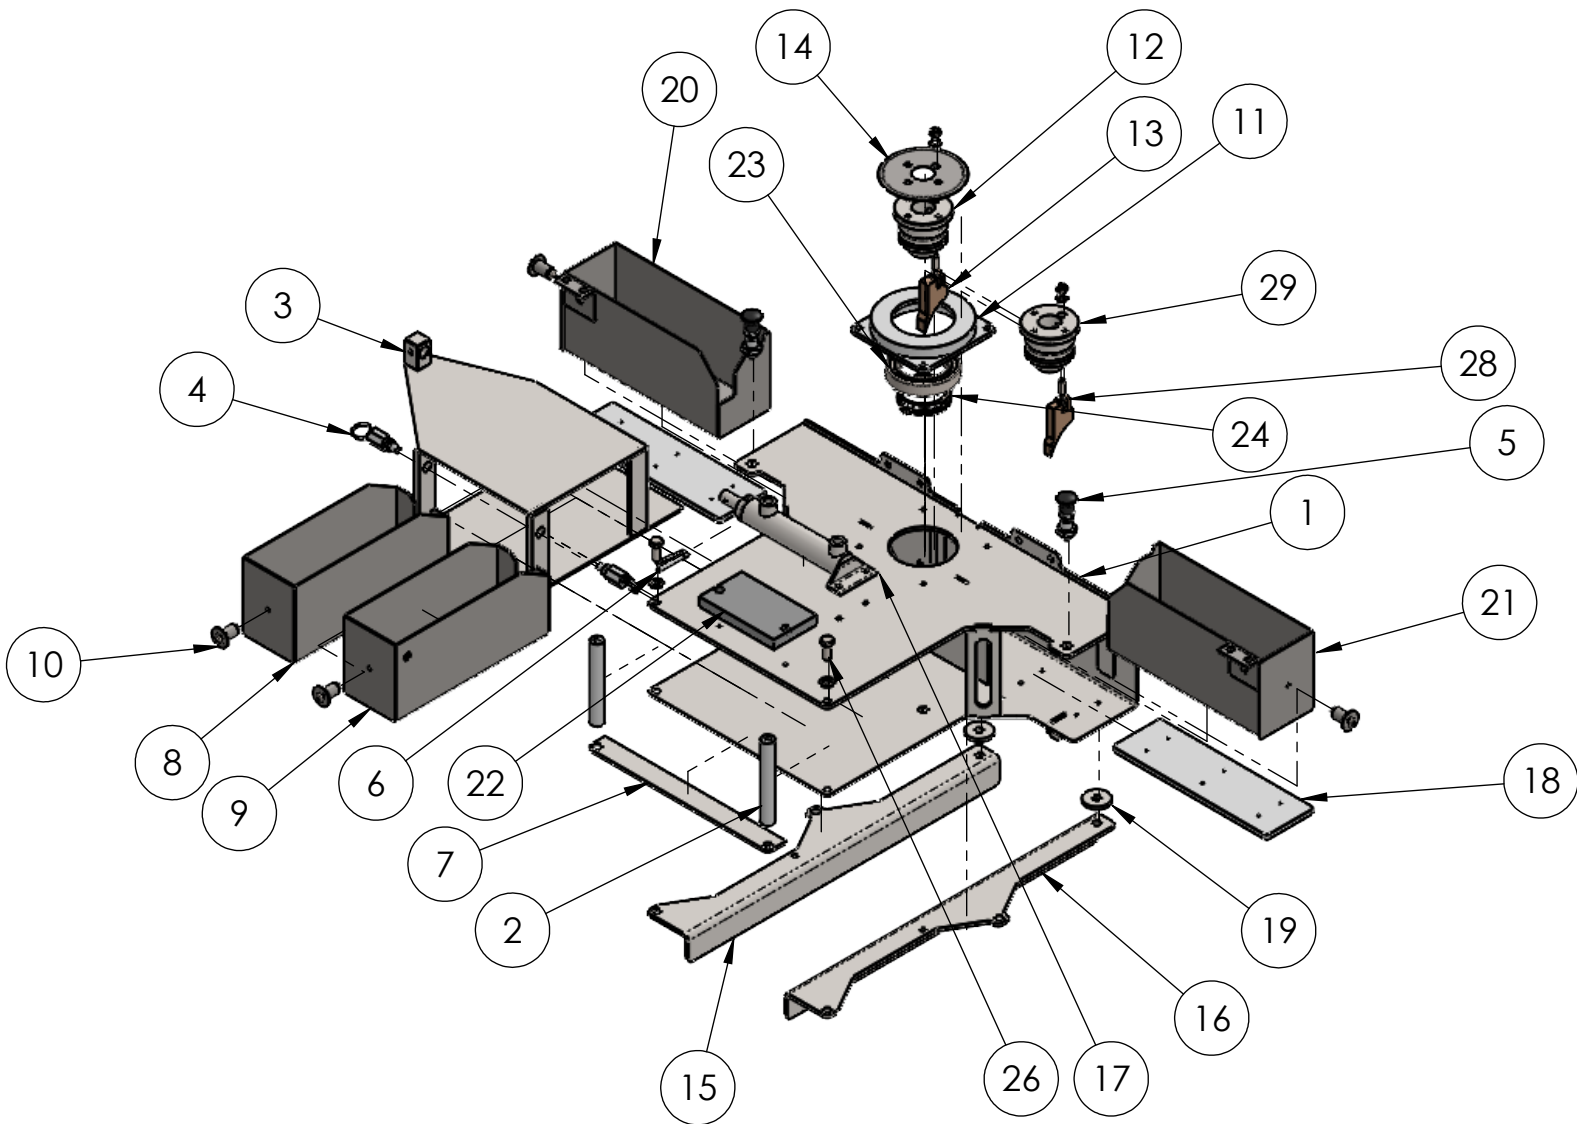

		Allgemeintoleranzen DIN ISO 2768-m-S	Werkstückkanten DIN 6784	WERKSTOFF: Bodenprobetechnik Peters GmbH Am Fliegerhorst 11 D-49610 Quakenbrück	MAßSTAB: 1:10 Tel.: 05431-936440 e-mail: info@bodenprobetechnik.de
NAME B.P.	DATUM 05.06.2023	ÄNDERUNGSTEXT Erstfreigabe		Magazin	
				ZEICHNUNGSNR. MP4.3	
				Technische Daten Schutzvermerk ISO 16016 beachten	A3
GEWICHT IN G: 35285.24		C:\Users\User\OneDrive - Bodenprobetechnik Peters GmbH\Fertigung\Zeichnungen\MP-1_2_3_4\MP.3_Magazin_FuB\			

POS-NR.	Artikel-nummer	Benennung	MENGE
1	UP.101.00-01	Laufrolle komplett	4
2	MP.400.00	Schlitten SBG	1
3	Z-MP.401.00	Hydraulikmotor 125	1
4	Z-MP.402.00	Hammerwerk	1
5	UP.403.04	Klemmsatz	1
6	MP-UP.405.00-02	Führungsnabe	1
7	UP.409.00-01	Verriegelungsbolzen	1
8	MP-UP.410.00	NL120E15K	1
9	MP-UP.418.00-01	Distanzring	2
10	MP-UP.419.00	Zahnrad	1
11	MP-UP.421.00-02	Zahnradabdeckung	1
12	MP.422.00	Verschleißblech Endlagensensor	1
13	Z-00022	Kotflügelscheibe	1
14	Z-00044	Sensor	3
15	Z-00067	Radialrillenkugellager	1
16	Z-00066	Sicherungsring außen	1
17	Z-00075	Zylinderschraube mit Innensechskant	4
18	Z-00078	Sicherungsring innen	1
19	Z-00082	Sechskantschraube	1
20	Z-00087	Unterlegscheibe	8
21	Z-00090	Sechskantmutter	2
22	Z-00092	Unterlegscheibe	4
23	Z-00111	Sensorkabel	3
24	Z-00124	Sechskantschraube mit Schaft	4
25	Z-00125	Sechskantmutter mit Klemnteile	4
26	Z-00	Zylinderkopfschraube mit Innensechskant	2
Seriennummern: HS3001 bis HS3005; HS3016-00.1			
28	Z-MP-UP.401.00	Hydraulikmotor 200	1
29	Z-UP.402.00	Hammerwerk LH11	1
30	UP.403.00-02	Klemmbacke für Hammerwerk	2
31	UP.403.01	Schraubensatz für Hammerwerk M10	1
32	UP.404.00	Schlagstößel lose	1
Alternative Bohrstöcke. Ausräumer und Ausräumnabe beachten!			
34	MP-UP.410.01	NL120E15Z	1
35	MP-UP.410.02	NL120E12K	1
36	MP-UP.410.03	NL120E12Z	1

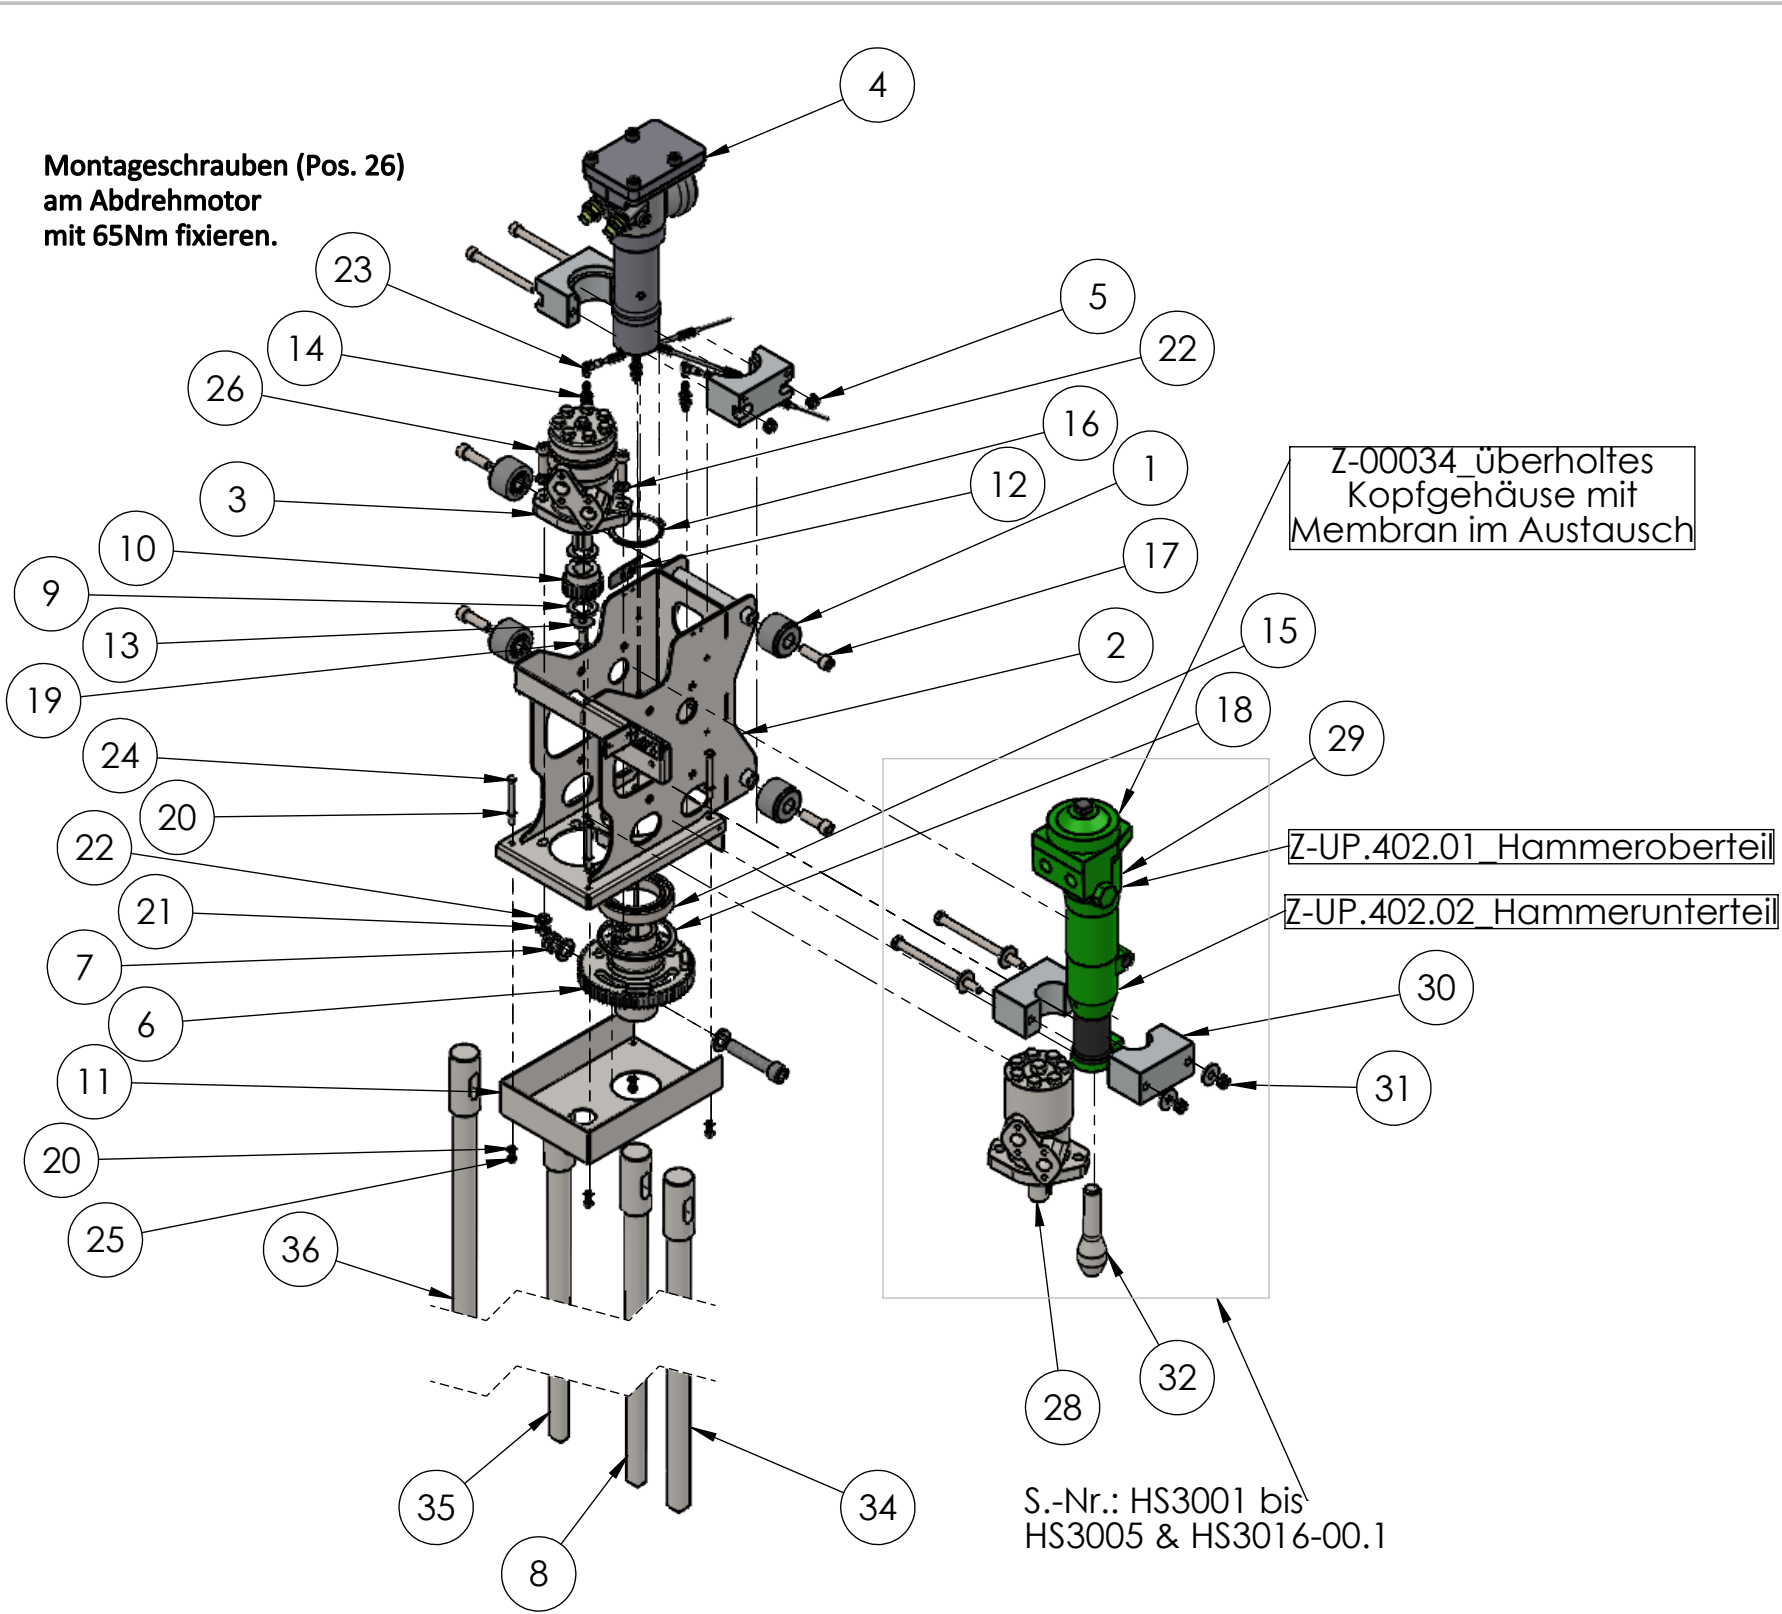

Allgemeintoleranzen
DIN ISO
2768-m-S

Werkstückkanten
DIN 6784


WERKSTOFF:
Bodenprobetechnik Peters GmbH
Am Fliegerhorst 11
D-49610 Quakenbrück
Tel.: 05431-936440
e-mail: info@bodenprobetechnik.de

MAßSTAB: 1:10

NAME	DATUM	ÄNDERUNGSTEXT
B.P.	05.06.2023	Erstfreigabe
GEWICHT IN G: 73098,73		

Schlitten	
ZEICHNUNGSNR. MP-1.120, MP-3.90, MP-4.100	
Technische Daten	A3
Schutzvermerk ISO 16016 beachten	
Blatt 1 v. 3	

POS-NR.	Artikelnummer	Benennung	MENGE
1	UP.101.00-01	Laufrolle komplett	4
2	MP.400.00	Schlitten SBG	1
3	Z-MP.401.00	Hydraulikmotor 125	1
4	Z-MP.402.00	Hammerwerk	1
5	UP.403.04	Klemmsatz	1
6	MP-UP.405.00-02	Führungsnahe	1
7	UP.409.00-01	Verriegelungsbolzen	1
8	DP-UP.410.00	NL60E15K	1
9	MP-UP.418.00-01	Distanzring	2
10	MP-UP.419.00	Zahnrad	1
11	MP-UP.421.00-02	Zahnradabdeckung	1
12	MP.422.00	Verschleißblech Endlagensensor	1
13	Z-00022	Kotflügelscheibe	1
14	Z-00044	Sensor	3
15	Z-00067	Radialrillenkugellager	1
16	Z-00066	Sicherungsring außen	1
17	Z-00075	Zylinderschraube mit Innensechskant	4
18	Z-00078	Sicherungsring innen	1
19	Z-00082	Sechskantschraube	1
20	Z-00087	Unterlegscheibe	8
21	Z-00090	Sechskantmutter	2
22	Z-00092	Unterlegscheibe	4
23	Z-00111	Sensorkabel	3
24	Z-00124	Sechskantschraube mit Schaft	4
25	Z-00125	Sechskantmutter mit Klemmteile	4
26	Z-00	Zylinderkopfschraube mit Innensechskant	2
Alternativer Bohrstocke. Ausräumer und Ausräumnahe beachten!			
28	DP-UP.411.00	NL60E12K	1

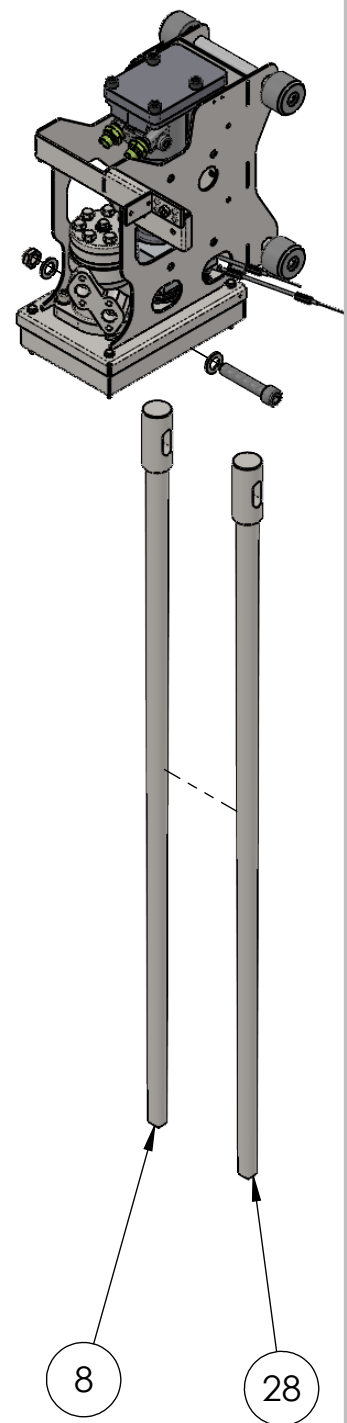

		Allgemeintoleranzen		Werkstückkanten		WERKSTOFF:		MABSTAB: 1:10	
		DIN ISO 2768-m-S		DIN 6784		Bodenprobetechnik Peters GmbH Am Fliegerhorst 11 D-49610 Quakenbrück		Tel.: 05431-936440 e-mail: info@bodenprobetechnik.de	
NAME	DATUM	ÄNDERUNGSTEXT		Schlitten					
B.P.	05.06.2023	Erstfreigabe							
				ZEICHNUNGSNR.					
				MP-1.90, MP-2.60					
				Technische Daten					
				Schutzvermerk ISO 16016 beachten					
				A4					
				Blatt 2 v. 3					
GEWICHT IN G: 73098.73				C:\Users\User\OneDrive - Bodenprobetechnik Peters GmbH\Fertigung\Zeichnungen\MP-1_2_3_4\MP.4_Schlitten\					

Schläuche MP-1.90/2.60/3.90/4.100/1.120

Artikelnummer	Anschlüsse	Menge
MP-UP.503.01	Section 1 Kanal A zu Hammerwerk (P)/ Section 3 Kanal A zu Abdrehmotor (Drosselrückschlagventil/links)	2
MP-UP.503.02	Hammerwerk (T) zu Fußplatte (T/Rücklauf)	1
MP-UP.503.03	Section 3 Kanal B zu Abdrehmotor (rechts)	1

Sägelänge in mm:

		Allgemeintoleranzen		Werkstückkanten		WERKSTOFF:		MABSTAB: 1:1	
		DIN ISO 2768-m-S		DIN 6784		Bodenprobetechnik Peters GmbH Tel.: 05433-6460 Bahnhofstr. 36 Fax: 05433-6444 D-49635 Badbergen e-mail: info@bodenprobetechnik.de			
NAME	DATUM	ÄNDERUNGSTEXT		MP Schläuche					
B. P.	02.08.2024	Erstfreigabe							
				ZEICHNUNGSNR. MP.503.00					
				Technische Daten Ersatzteilliste					
				A4					
GEWICHT IN G:		C:\Users\User\OneDrive - Bodenprobetechnik Peters GmbH\Fertigung\Zeichnungen\MP-1_2_3_4\MP.5_Ventilblock und -leitungen\MP.503.00_Schläuche\							